


APPARTAMENTO - posa gres 60x60

origine di posa ottimale 26.1 / 54.0 cm - minimo numero di lastre e di tagli; rivestimento bagno su 4 corsi a filo trave
fuga 1.5 mm - modulo 60.15 cm - griglia unica continua su tutta la casa - battiscopa/rivestimento 1 cm - origine 26.1/54.0 - stampa 100% = 1:60

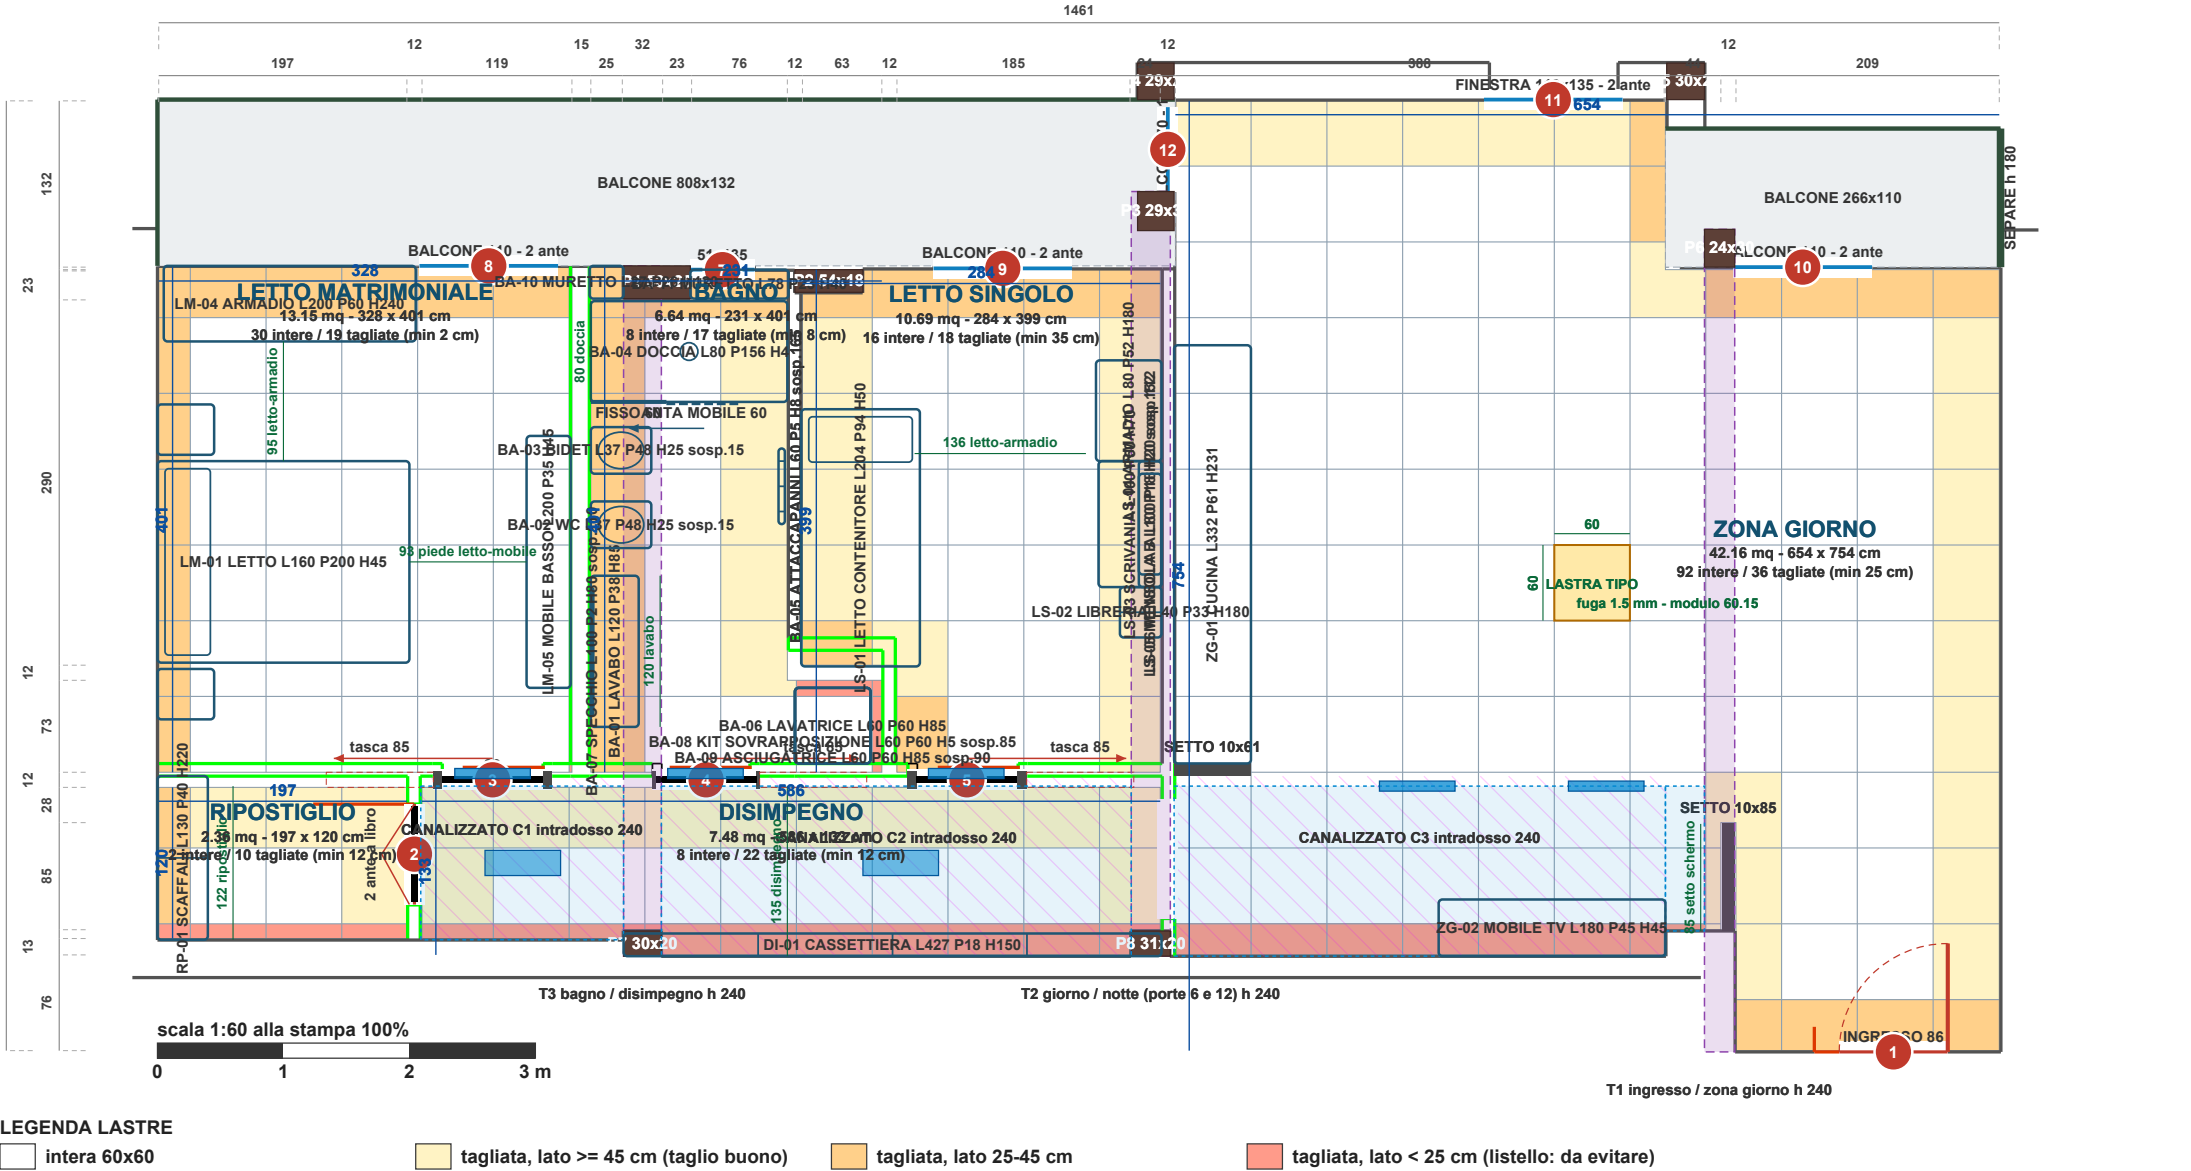

CONFRONTO FORMATI (ognuno con la sua origine di posa ottimale)										
formato	origine X/Y	lastre intere	tagliate	tagli < 25 cm	tagli 25-45	tagli > 45	lato minimo	% sup. con intere	lastre / sfrido	
90x90, 3 corsi a filo trave	27.4 / 29.4	51	93	5	40	48	7 cm	50%	122	17%
80x80, 3 corsi a filo trave	19.3 / 59.0	76	93	30	5	58	10 cm	59%	152	15%
60x60, 4 corsi a filo trave	26.1 / 54.0	156	122	31	40	51	2 cm	68%	258	11%