


APPARTAMENTO - posa gres 80x80

origine di posa ottimale 37.7 / 59.0 cm - minimo numero di lastre e di tagli; rivestimento bagno su 4 corsi a filo trave
fuga 1.5 mm - modulo 80.15 cm - griglia unica continua su tutta la casa - battiscopa/rivestimento 1 cm - origine 37.7/59.0 - stampa 100% = 1:60

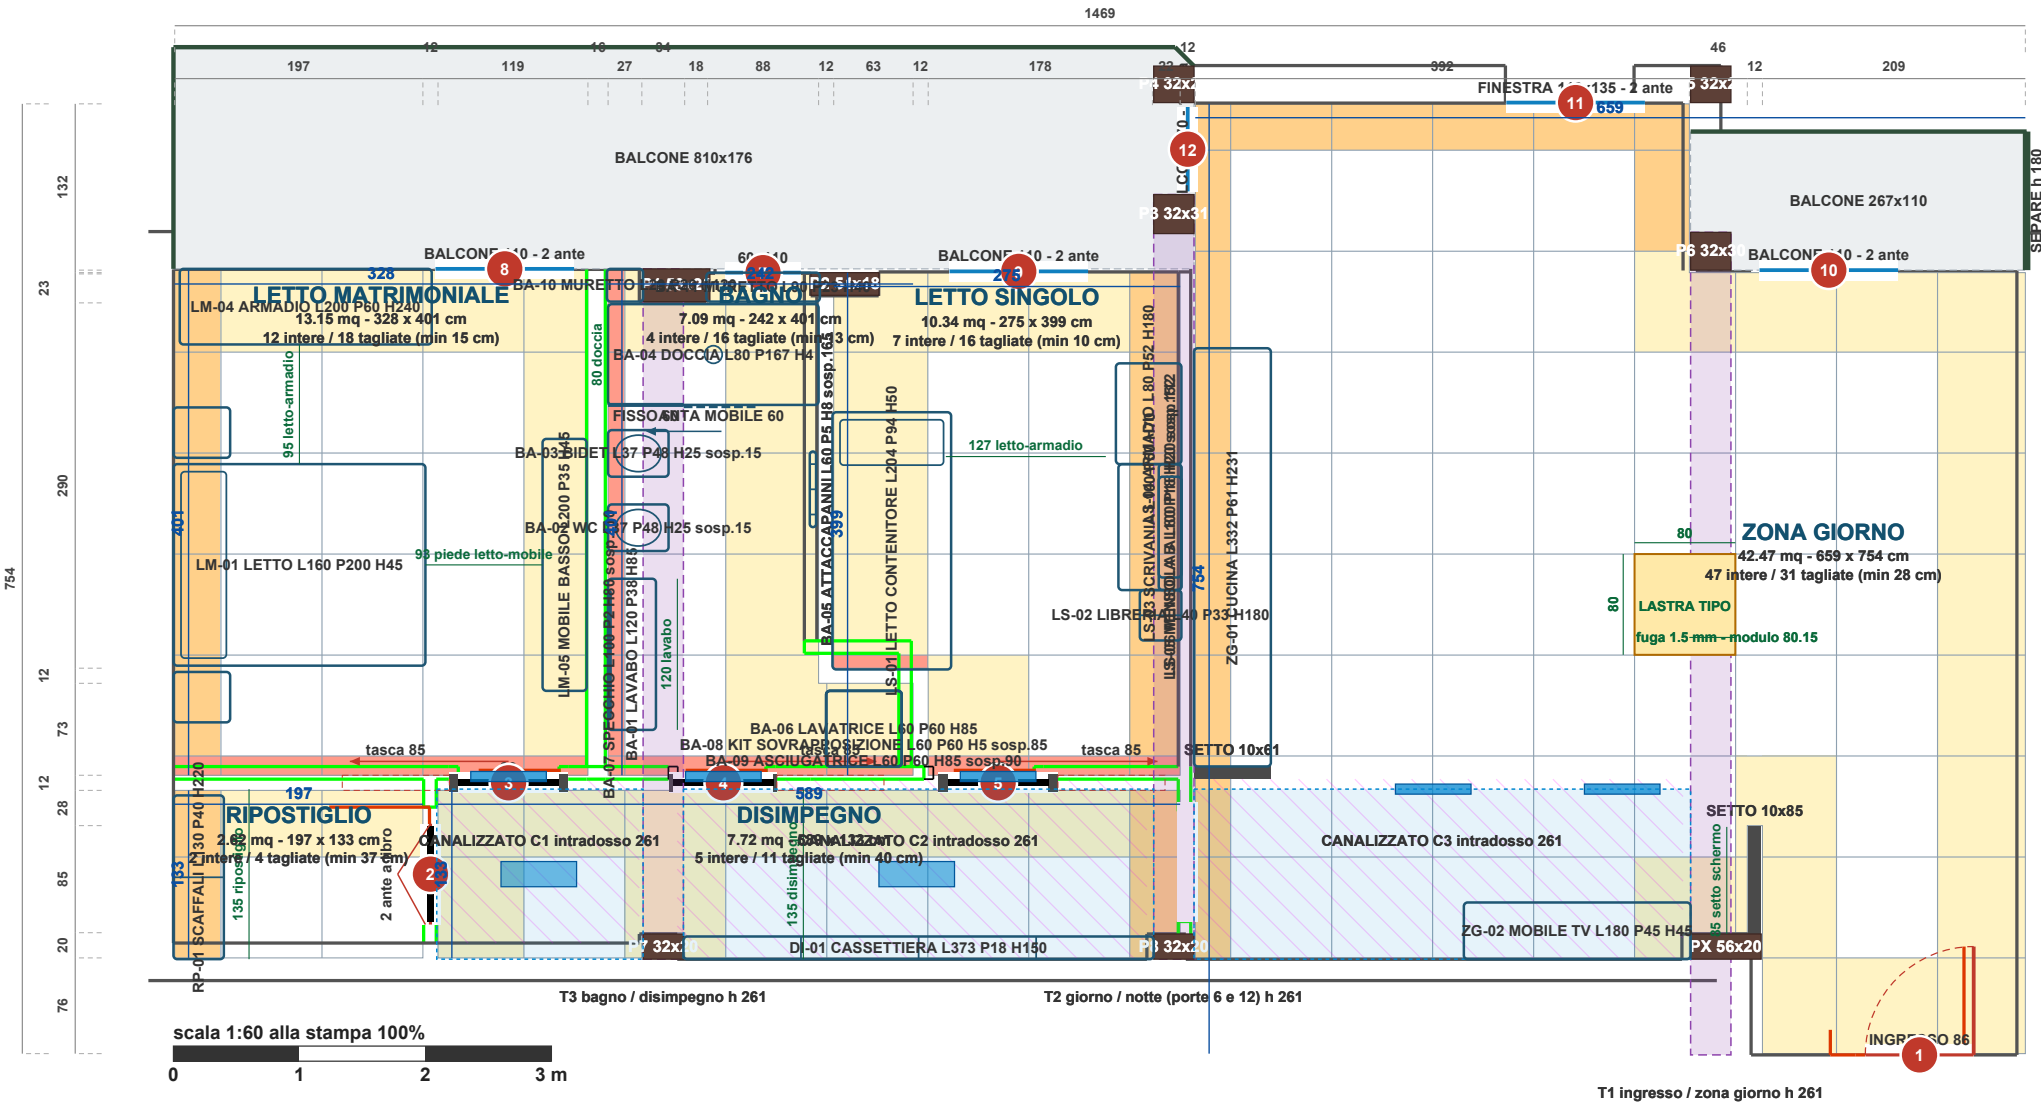

LEGENDA LASTRE

- intera 80x80
- tagliata, lato >= 45 cm (taglio buono)
- tagliata, lato 25-45 cm
- tagliata, lato < 25 cm (listello: da evitare)

CONFRONTO FORMATI (ognuno con la sua origine di posa ottimale)

formato	origine X/Y	lastre intere	tagliate	tagli < 25 cm	tagli 25-45	tagli > 45	lato minimo	% sup. con intere	lastre / sfrido
90x90, 3 corsi a filo trave	27.6 / 24.2	63	83	3	45	35	4 cm	61%	123 / 16%
80x80, 4 corsi a filo trave	37.7 / 59.0	77	96	18	29	49	10 cm	59%	151 / 14%
60x60, 5 corsi a filo trave	29.1 / 54.0	155	121	28	34	59	2 cm	67%	259 / 11%