


APPARTAMENTO - posa gres 60x60

origine di posa ottimale 29.1 / 54.0 cm - minimo numero di lastre e di tagli; rivestimento bagno su 5 corsi a filo trave  
fuga 1.5 mm - modulo 60.15 cm - griglia unica continua su tutta la casa - battiscopa/rivestimento 1 cm - origine 29.1/54.0 - stampa 100% = 1:60

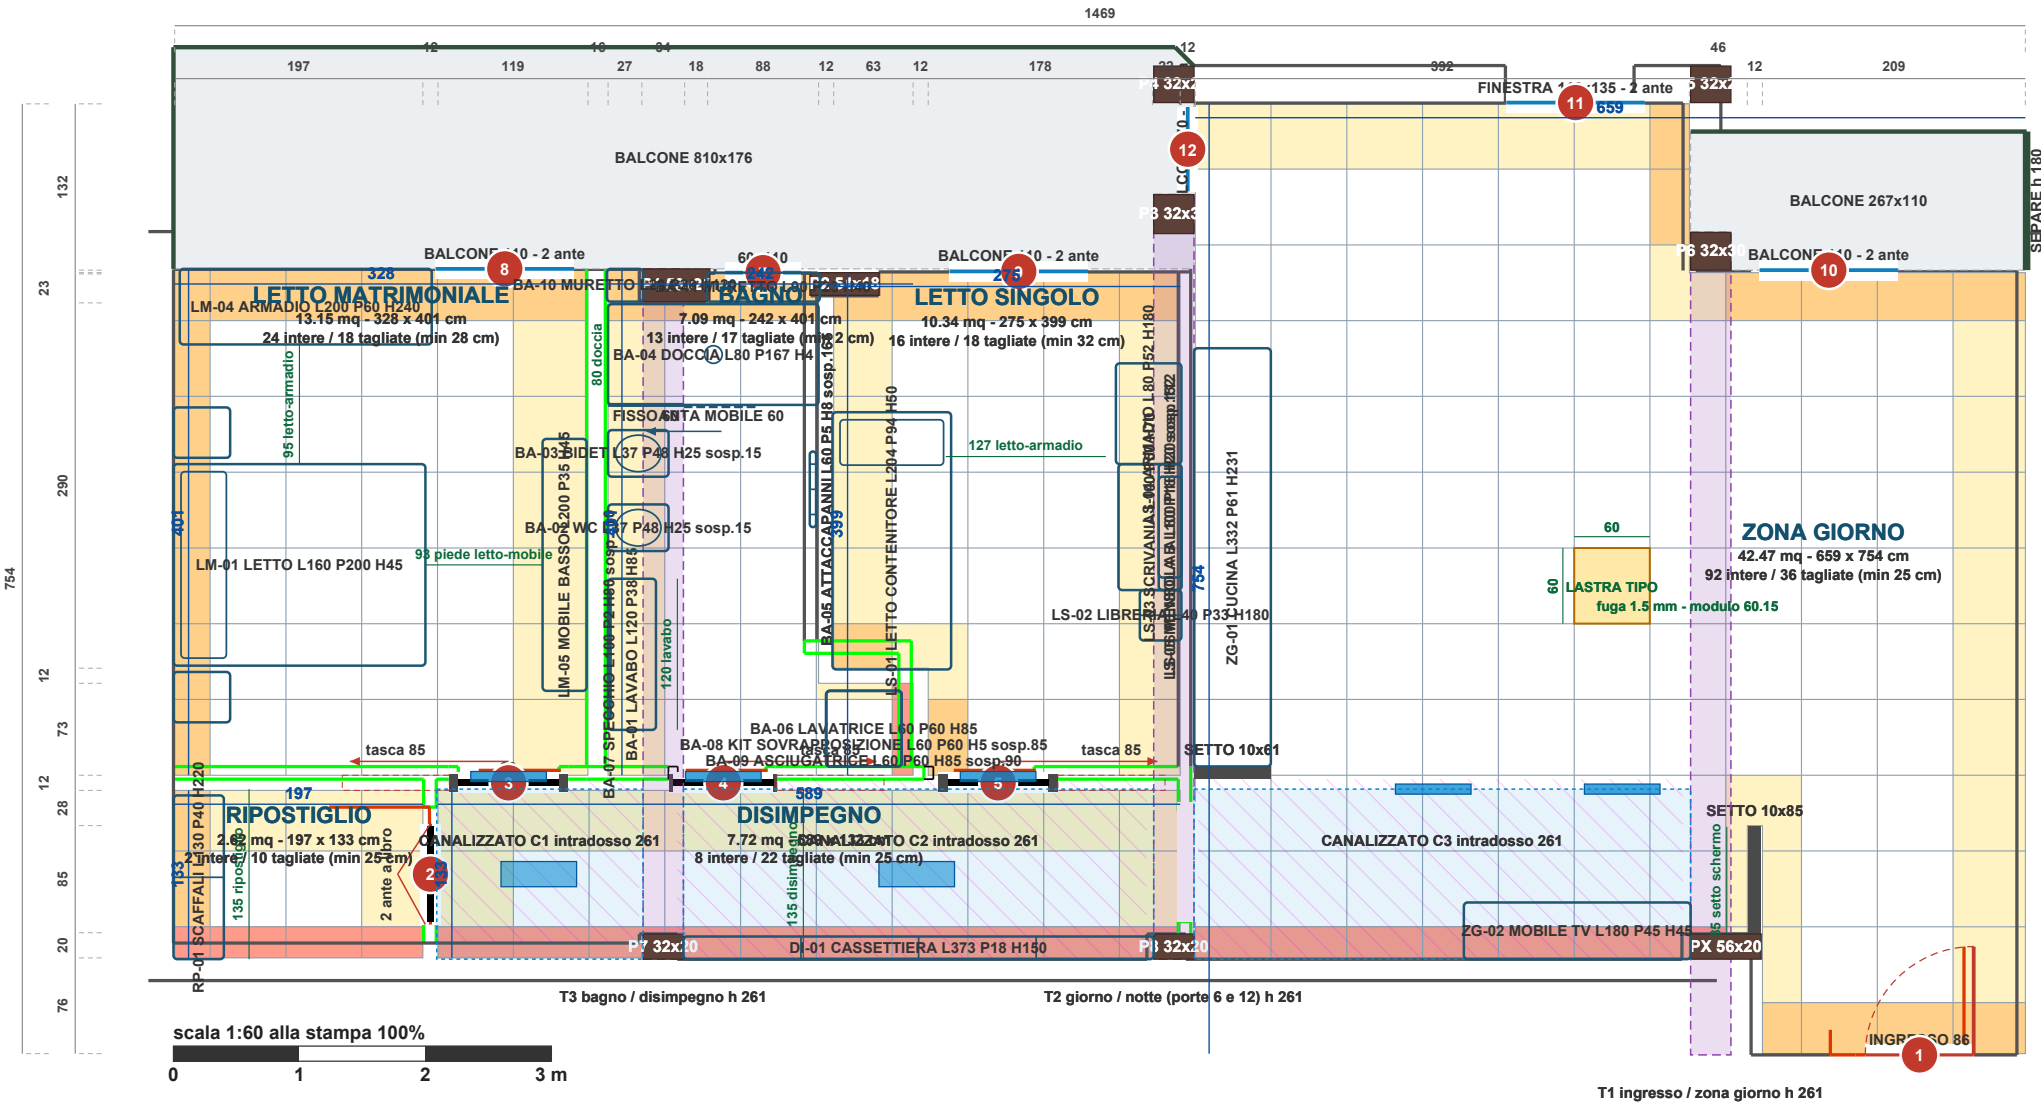

LEGENDA LASTRE

- intera 60x60
- tagliata, lato >= 45 cm (taglio buono)
- tagliata, lato 25-45 cm
- tagliata, lato < 25 cm (listello: da evitare)

CONFRONTO FORMATI (ognuno con la sua origine di posa ottimale)

| formato                     | origine X/Y | lastre intere | tagliate | tagli < 25 cm | tagli 25-45 | tagli > 45 | lato minimo | % sup. con intere | lastre / sfrido |
|-----------------------------|-------------|---------------|----------|---------------|-------------|------------|-------------|-------------------|-----------------|
| 90x90, 3 corsi a filo trave | 27.6 / 24.2 | 63            | 83       | 3             | 45          | 35         | 4 cm        | 61%               | 123 / 16%       |
| 80x80, 4 corsi a filo trave | 37.7 / 59.0 | 77            | 96       | 18            | 29          | 49         | 10 cm       | 59%               | 151 / 14%       |
| 60x60, 5 corsi a filo trave | 29.1 / 54.0 | 155           | 121      | 28            | 34          | 59         | 2 cm        | 67%               | 259 / 11%       |