


BAGNO - ipotesi di arredo in scala 1:20

Rilievo da TAV 02 "Stato di progetto" - vano netto 1,58 x 3,95 m (6,75 mq) con nicchia 0,90 x 0,75 m

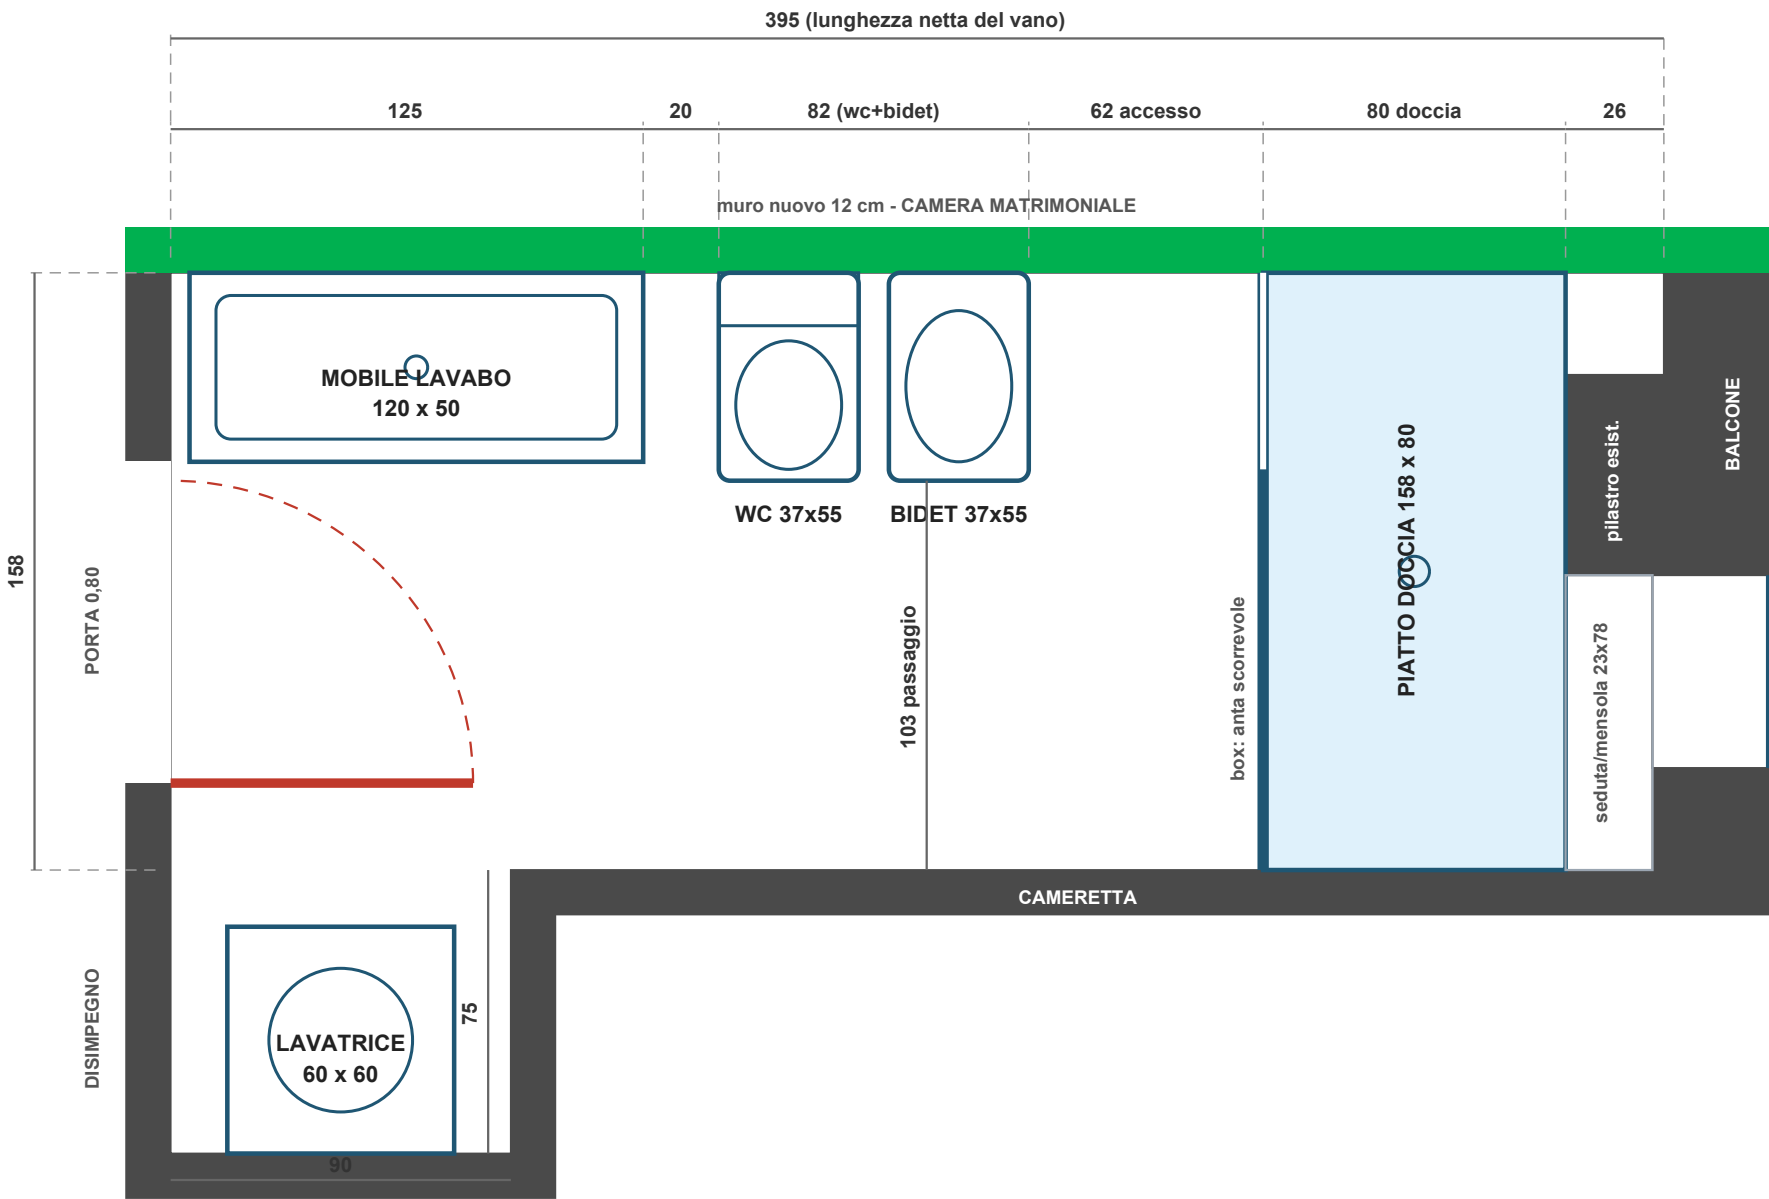

Interasse wc-bidet 45 cm - luce libera laterale ≥ 20 cm - spazio frontale sanitari 103 cm - accesso doccia 62 cm. Finestra 0,51 x 0,89 con davanzale a 1,35 m (ricade n
Piatto doccia su misura 158x80 a filo del pilastro; la nicchia 23x78 sotto la finestra va tamponata (seduta/mensola h 45) oppure inclusa in un piatto sagomato.
Porta 0,80 con apertura verso l'interno lato nicchia (non interferisce con il mobile lavabo): valutare scorrevole esterno muro.