


APPARTAMENTO - posa gres 90x90 | variante A

A - equilibrata: minimizza i listelli in tutta la casa (zona giorno pesata x4)
fuga 1.5 mm - modulo 90.15 cm - griglia unica continua su tutta la casa - battiscopa/rivestimento 1 cm - origine 59.5/32.1 - stampa 100% = 1:60

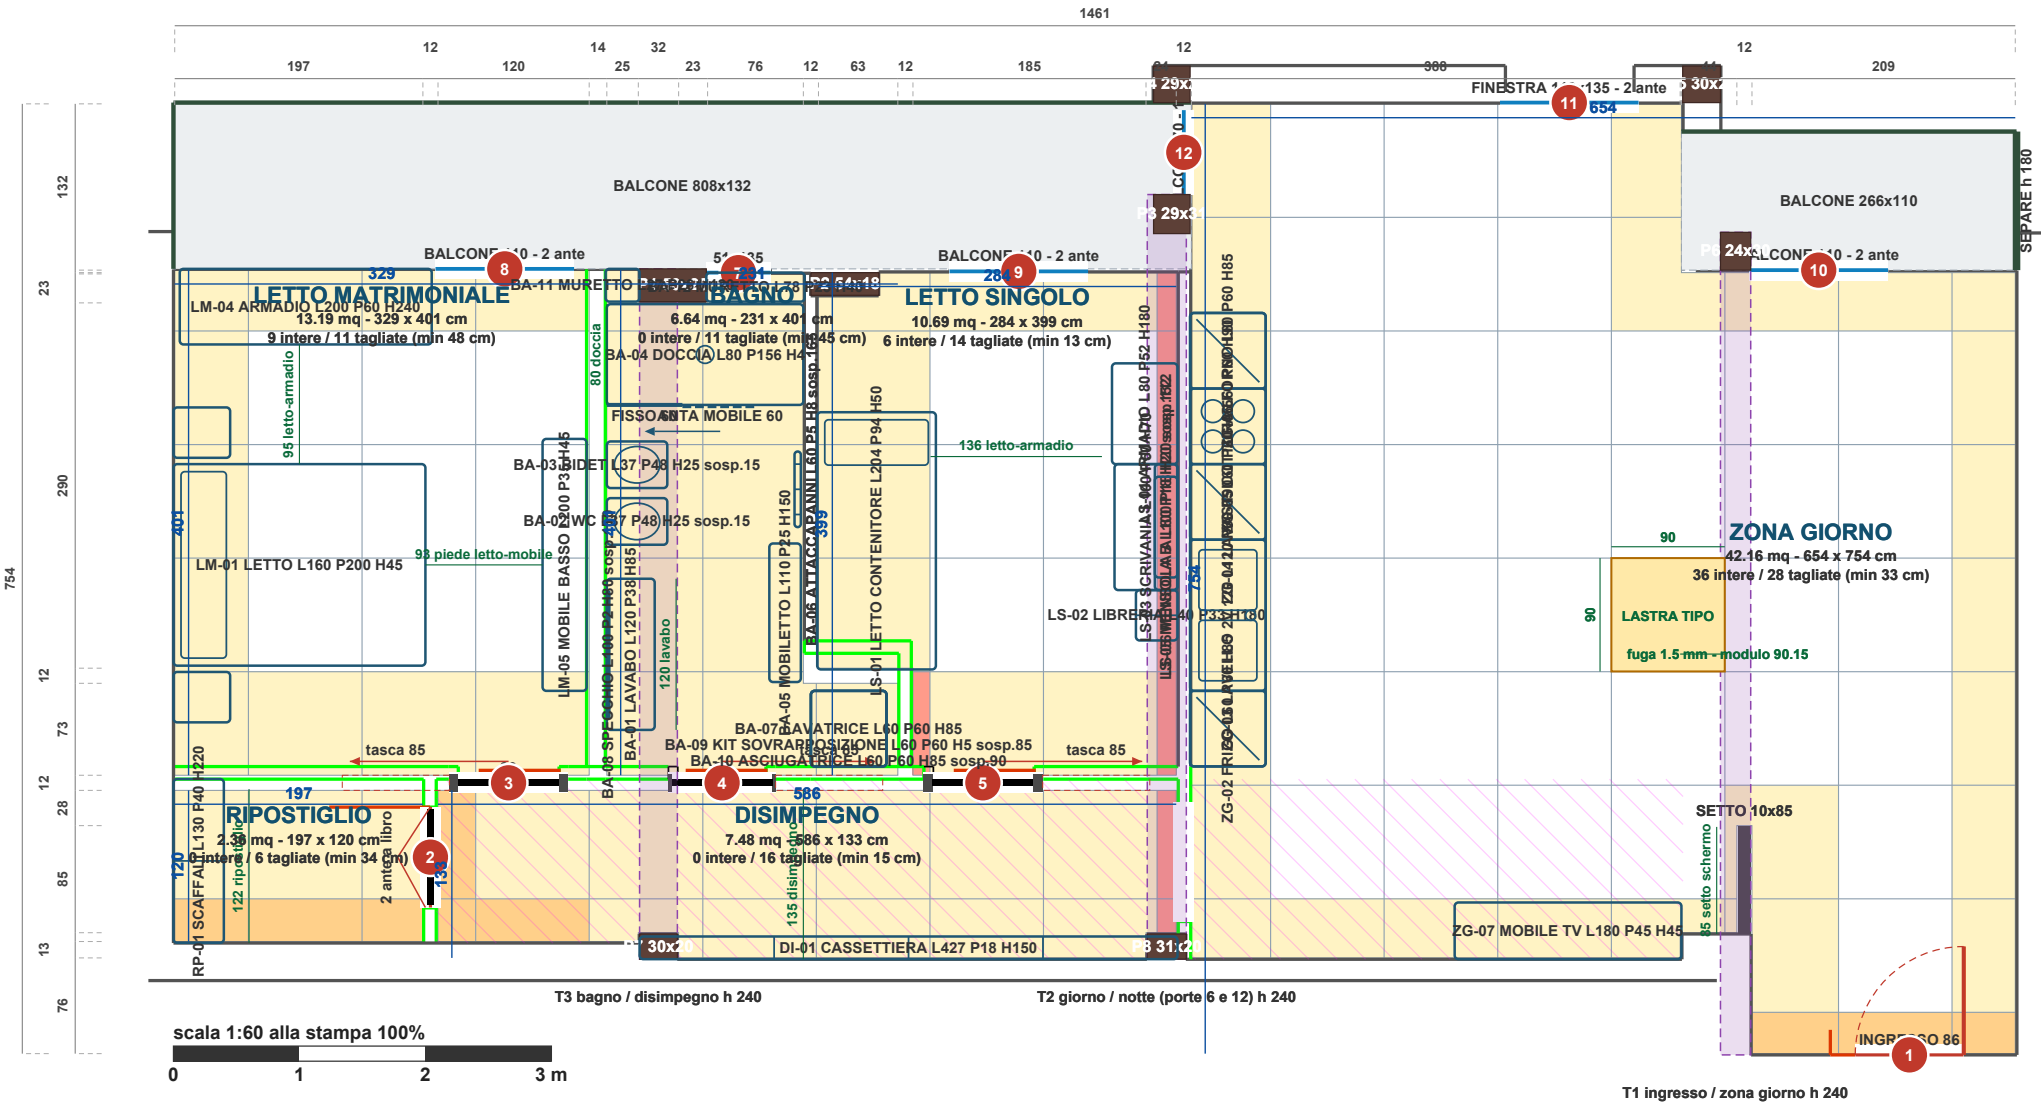

LEGENDA LASTRE

- intera 90x90
- tagliata, lato >= 45 cm (taglio buono)
- tagliata, lato 25-45 cm
- tagliata, lato < 25 cm (listello: da evitare)

CONFRONTO VARIANTI (stessi dati del disegno)

variante	origine X/Y	lastre intere	tagliate	tagli < 25 cm	tagli 25-45	tagli > 45	lato minimo	% sup. con intere	lastre / sfrido
A	59.5 / 32.1	51	86	8	9	69	13 cm	50%	130 / 22%
B	86.8 / 65.0	62	90	29	21	40	1 cm	61%	129 / 21%
C	86.8 / 32.2	58	82	16	13	53	6 cm	57%	126 / 19%