


APPARTAMENTO - posa gres 60x60, 4 corsi a 240

origine di posa ottimale 28.5 / 53.6 cm - minimo numero di lastre e di tagli; rivestimento bagno su 4 corsi a 240  
fuga 2.0 mm - modulo 60.20 x 60.20 cm - griglia unica continua su tutta la casa - battiscopa/rivestimento 1 cm - origine 28.5/53.6 - stampa 100% = 1:60

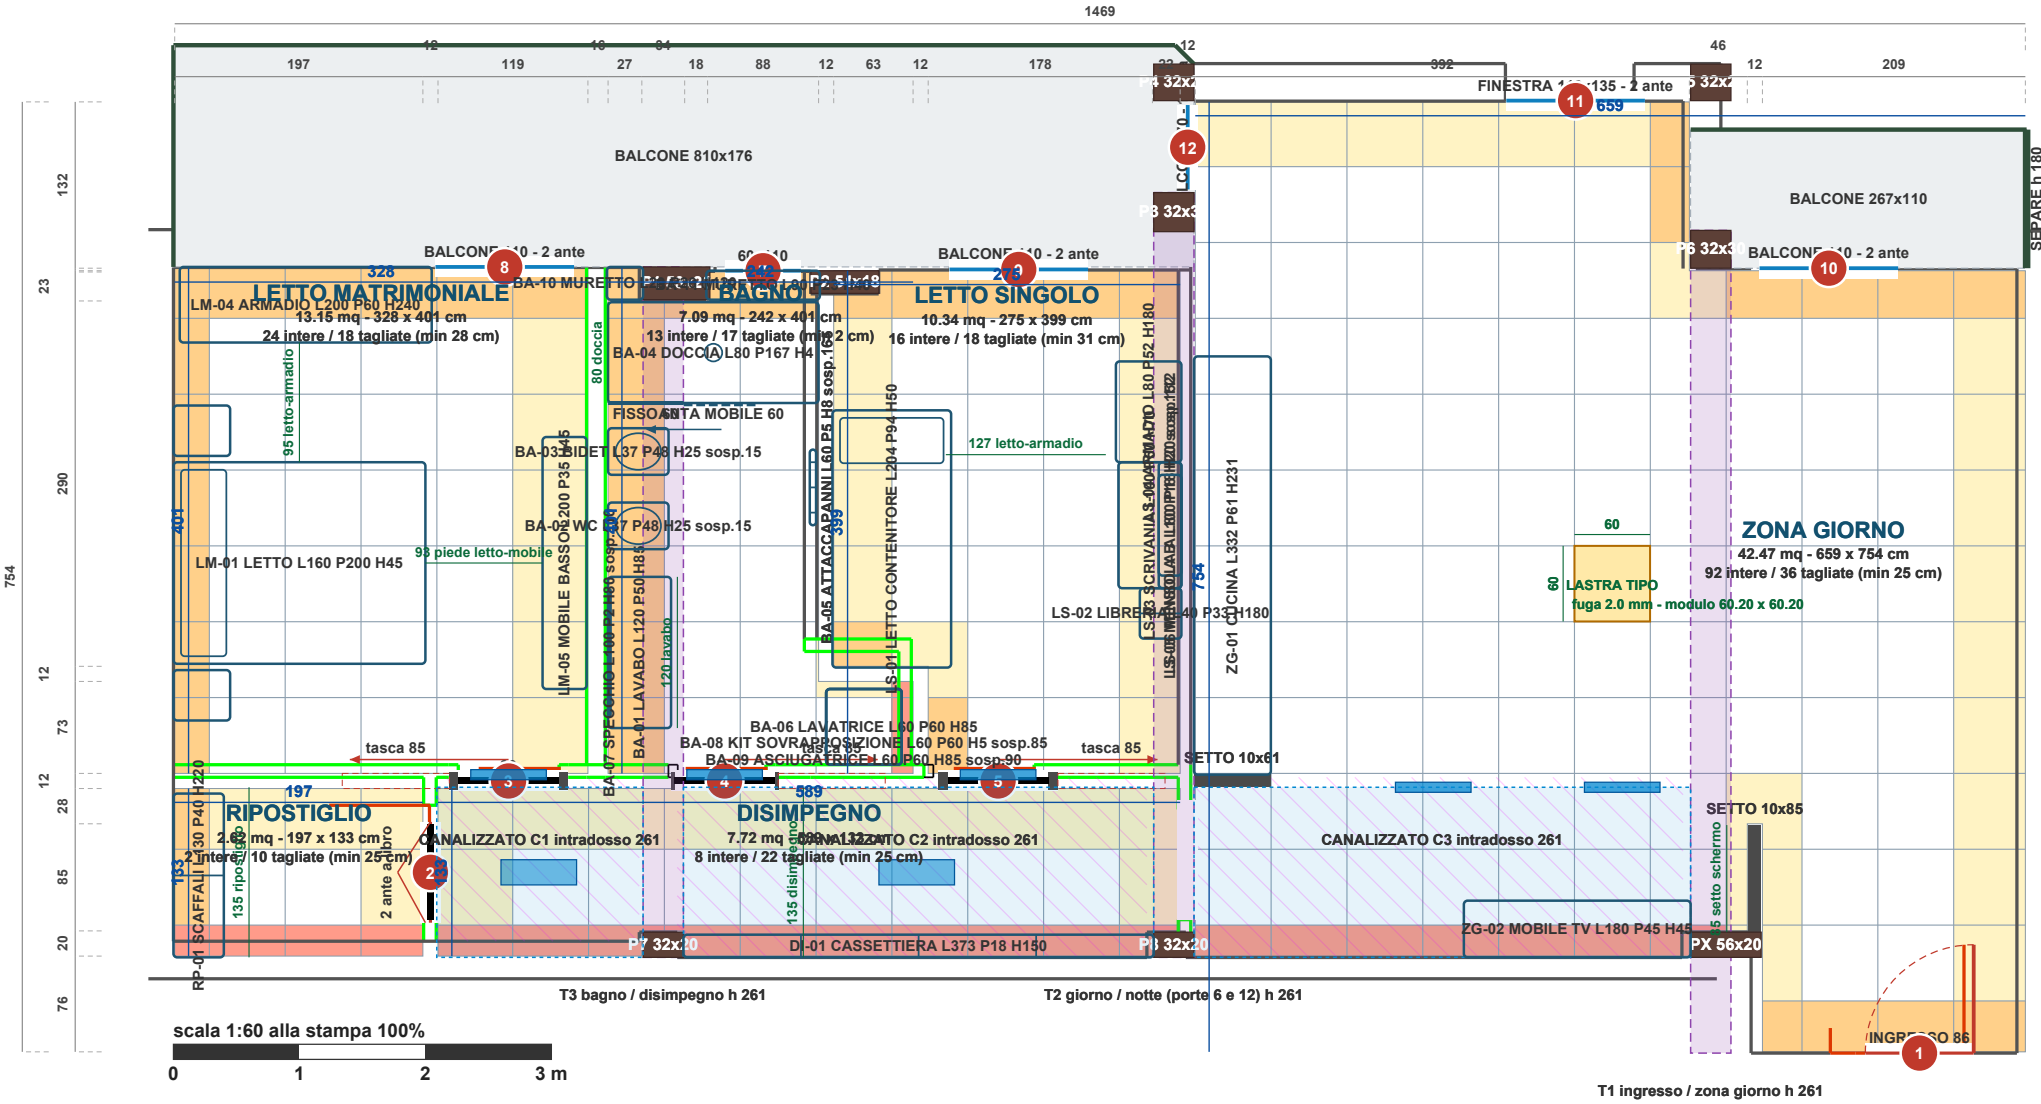

LEGENDA LASTRE

- intera 60x60
- tagliata, lato >= 45 cm (taglio buono)
- tagliata, lato 25-45 cm
- tagliata, lato < 25 cm (listello: da evitare)

| CONFRONTO FORMATI (ognuno con la sua origine di posa ottimale) |              |               |          |               |             |            |             |                   |                 |
|----------------------------------------------------------------|--------------|---------------|----------|---------------|-------------|------------|-------------|-------------------|-----------------|
| formato                                                        | origine X/Y  | lastre intere | tagliate | tagli < 25 cm | tagli 25-45 | tagli > 45 | lato minimo | % sup. con intere | lastre / sfrido |
| 90x90, 3 corsi a filo trave                                    | 26.8 / 24.0  | 63            | 83       | 3             | 45          | 35         | 4 cm        | 61%               | 123 / 16%       |
| 80x80, 4 corsi a filo trave                                    | 37.7 / 74.0  | 70            | 90       | 5             | 25          | 60         | 14 cm       | 54%               | 148 / 12%       |
| 60x60, 4 corsi a 240                                           | 28.5 / 53.6  | 155           | 121      | 28            | 40          | 53         | 2 cm        | 67%               | 259 / 11%       |
| 60x120, 2 corsi a 240                                          | 28.5 / 62.2  | 60            | 95       | 4             | 16          | 75         | 2 cm        | 52%               | 136 / 15%       |
| 60x120 pav 120x60 par, 4 corsi a 240                           | 28.5 / 62.2  | 60            | 95       | 4             | 16          | 75         | 2 cm        | 52%               | 136 / 15%       |
| 120x60 pav 60x120 par, 2 corsi a 240                           | 88.6 / 53.6  | 55            | 94       | 12            | 16          | 66         | 13 cm       | 47%               | 134 / 14%       |
| 120x60, 4 corsi a 240                                          | 88.6 / 53.6  | 55            | 94       | 12            | 16          | 66         | 13 cm       | 47%               | 134 / 14%       |
| 120x120, 2 corsi a 240, intera all'ingresso                    | 118.3 / 95.0 | 31            | 76       | 23            | 29          | 24         | 3 cm        | 54%               | 82 / 29%        |
| 60x120, 2 corsi a 240, a filo bagno                            | 30.5 / 6.2   | 71            | 97       | 32            | 7           | 58         | 1 cm        | 61%               | 142 / 18%       |
| 120x60, 4 corsi a 240, a filo bagno                            | 31.3 / 5.4   | 63            | 103      | 18            | 12          | 73         | 3 cm        | 54%               | 139 / 17%       |
| 120x60, 4 corsi a 240, per stanza                              | 27.6 / 33.8  | 82            | 68       | 11            | 18          | 39         | 12 cm       | 70%               | 134 / 13%       |
| 60x120, 2 corsi a 240, per stanza                              | 28.5 / 62.2  | 84            | 73       | 20            | 24          | 29         | 11 cm       | 72%               | 137 / 15%       |