PIANTA GENERALE - scala 1:50 (A3)

Posa pavimento #5 (ordine di sfrido del modello 3D): gres 120x60, sfalsata 1/2, fuga 2 mm, origine griglia 29,1 / 53,6 - 134 lastre (96,5 mq), 57 intere, 101 tagliate, sfrido 13,6%

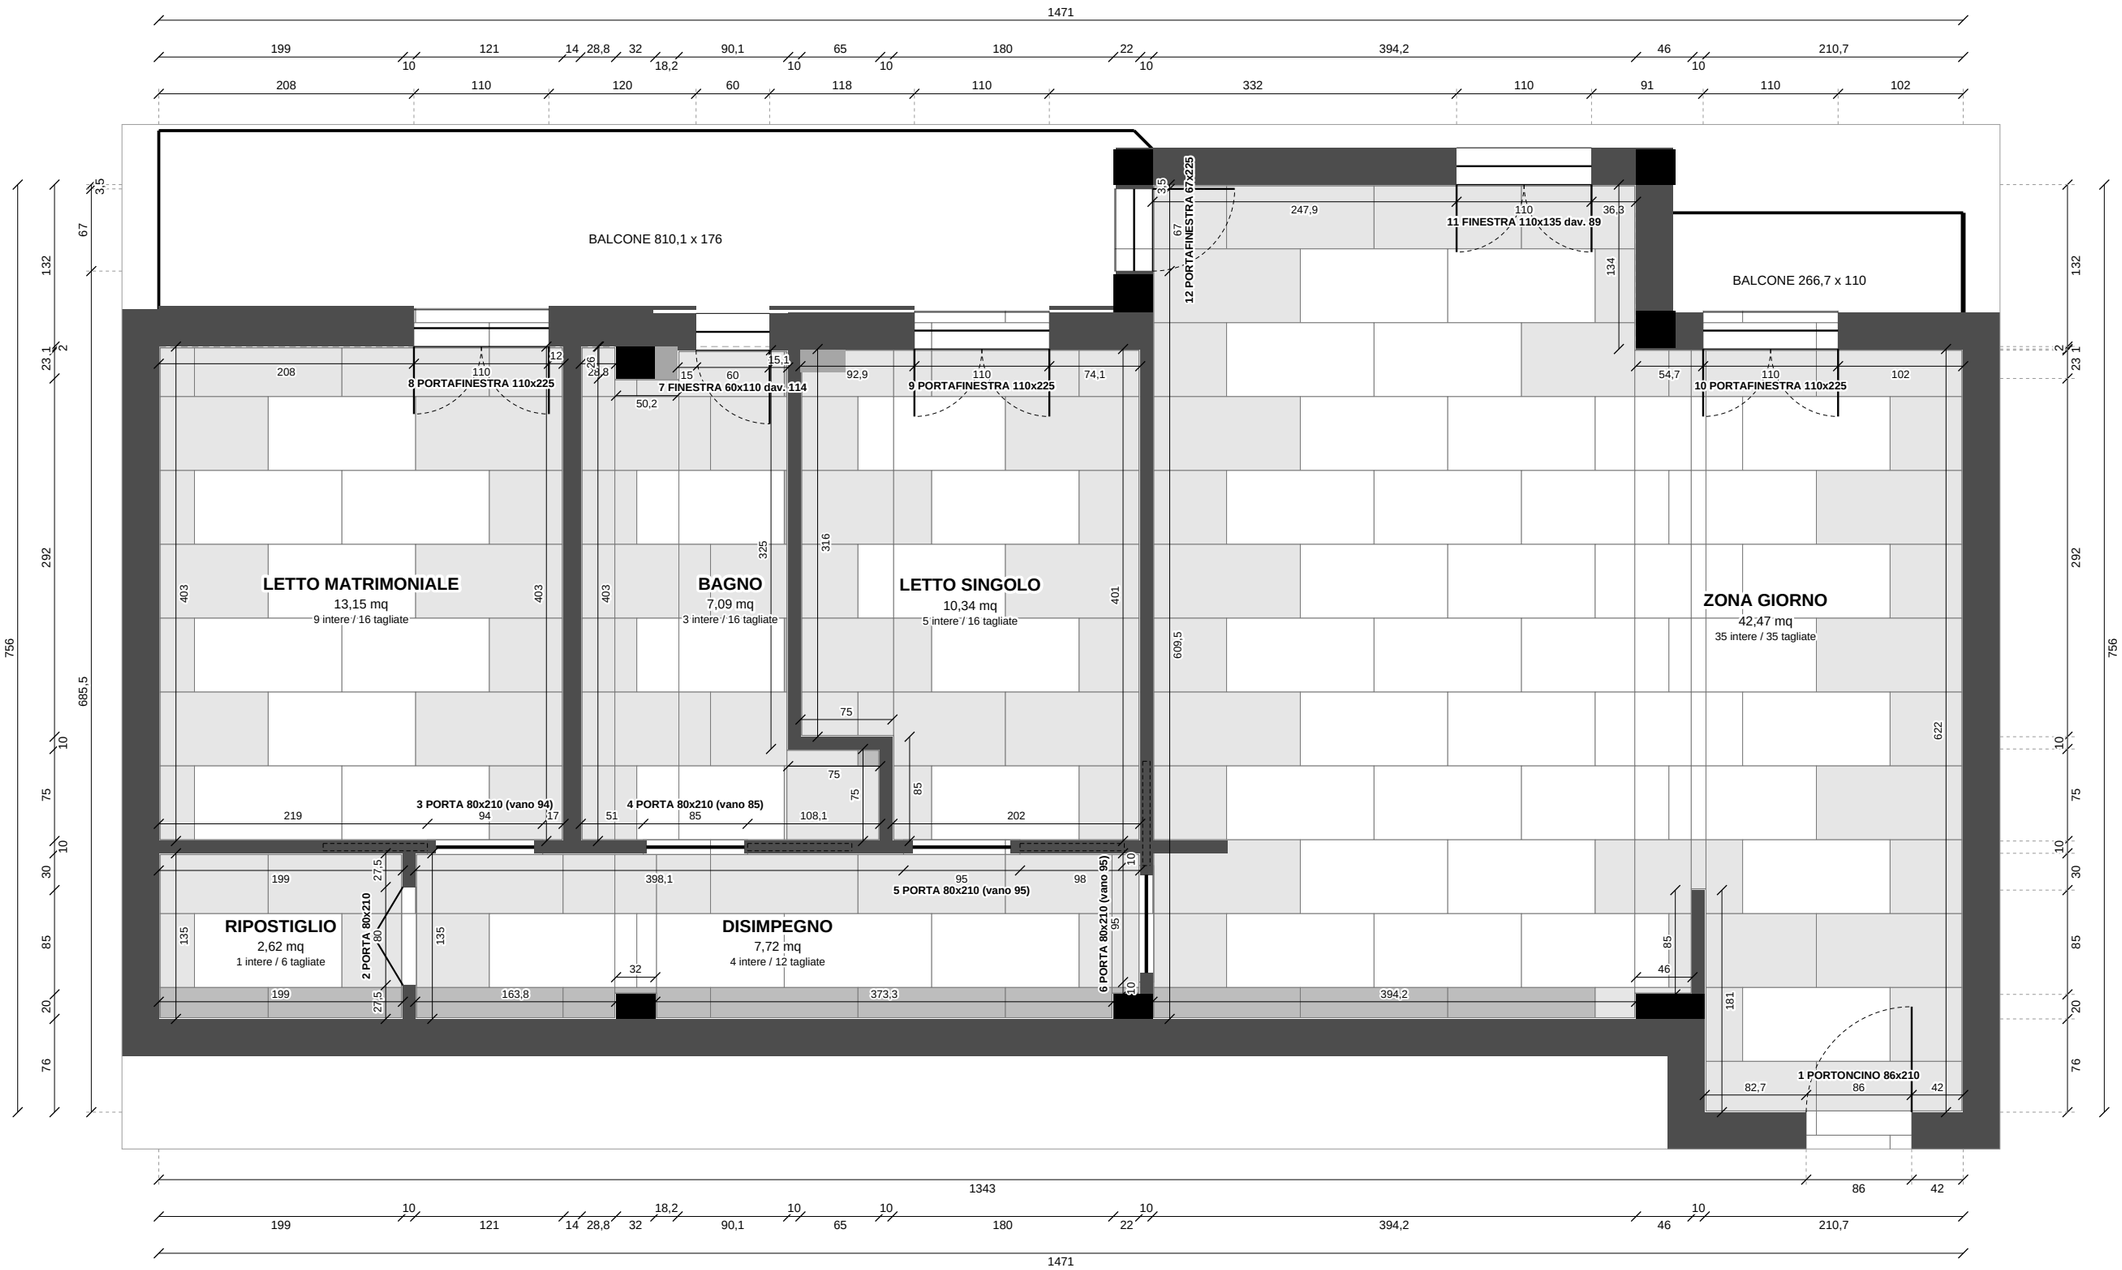

0 1 2 3 4 5 m

lastra intera 120x60 | lastra tagliata | listello, lato < 25 cm | muri sezionati a 150 cm | pilastri in c.a.

quote in cm al filo muro (prima di rivestimento e battiscopa); dentro i locali le misure di ogni lato con le aperture, fuori le catene di facciata; porte a scomparsa con tasca tratteggiata

ZONA GIORNO - soggiorno, cucina, ingresso - scala 1:30 (A3)

Posa pavimento #5 (ordine di sfrido del modello 3D): gres 120x60, sfalsata 1/2, fuga 2 mm, origine griglia 29,1 / 53,6 - 134 lastre (96,5 mq), 57 intere, 101 tagliate, sfrido 13,6%

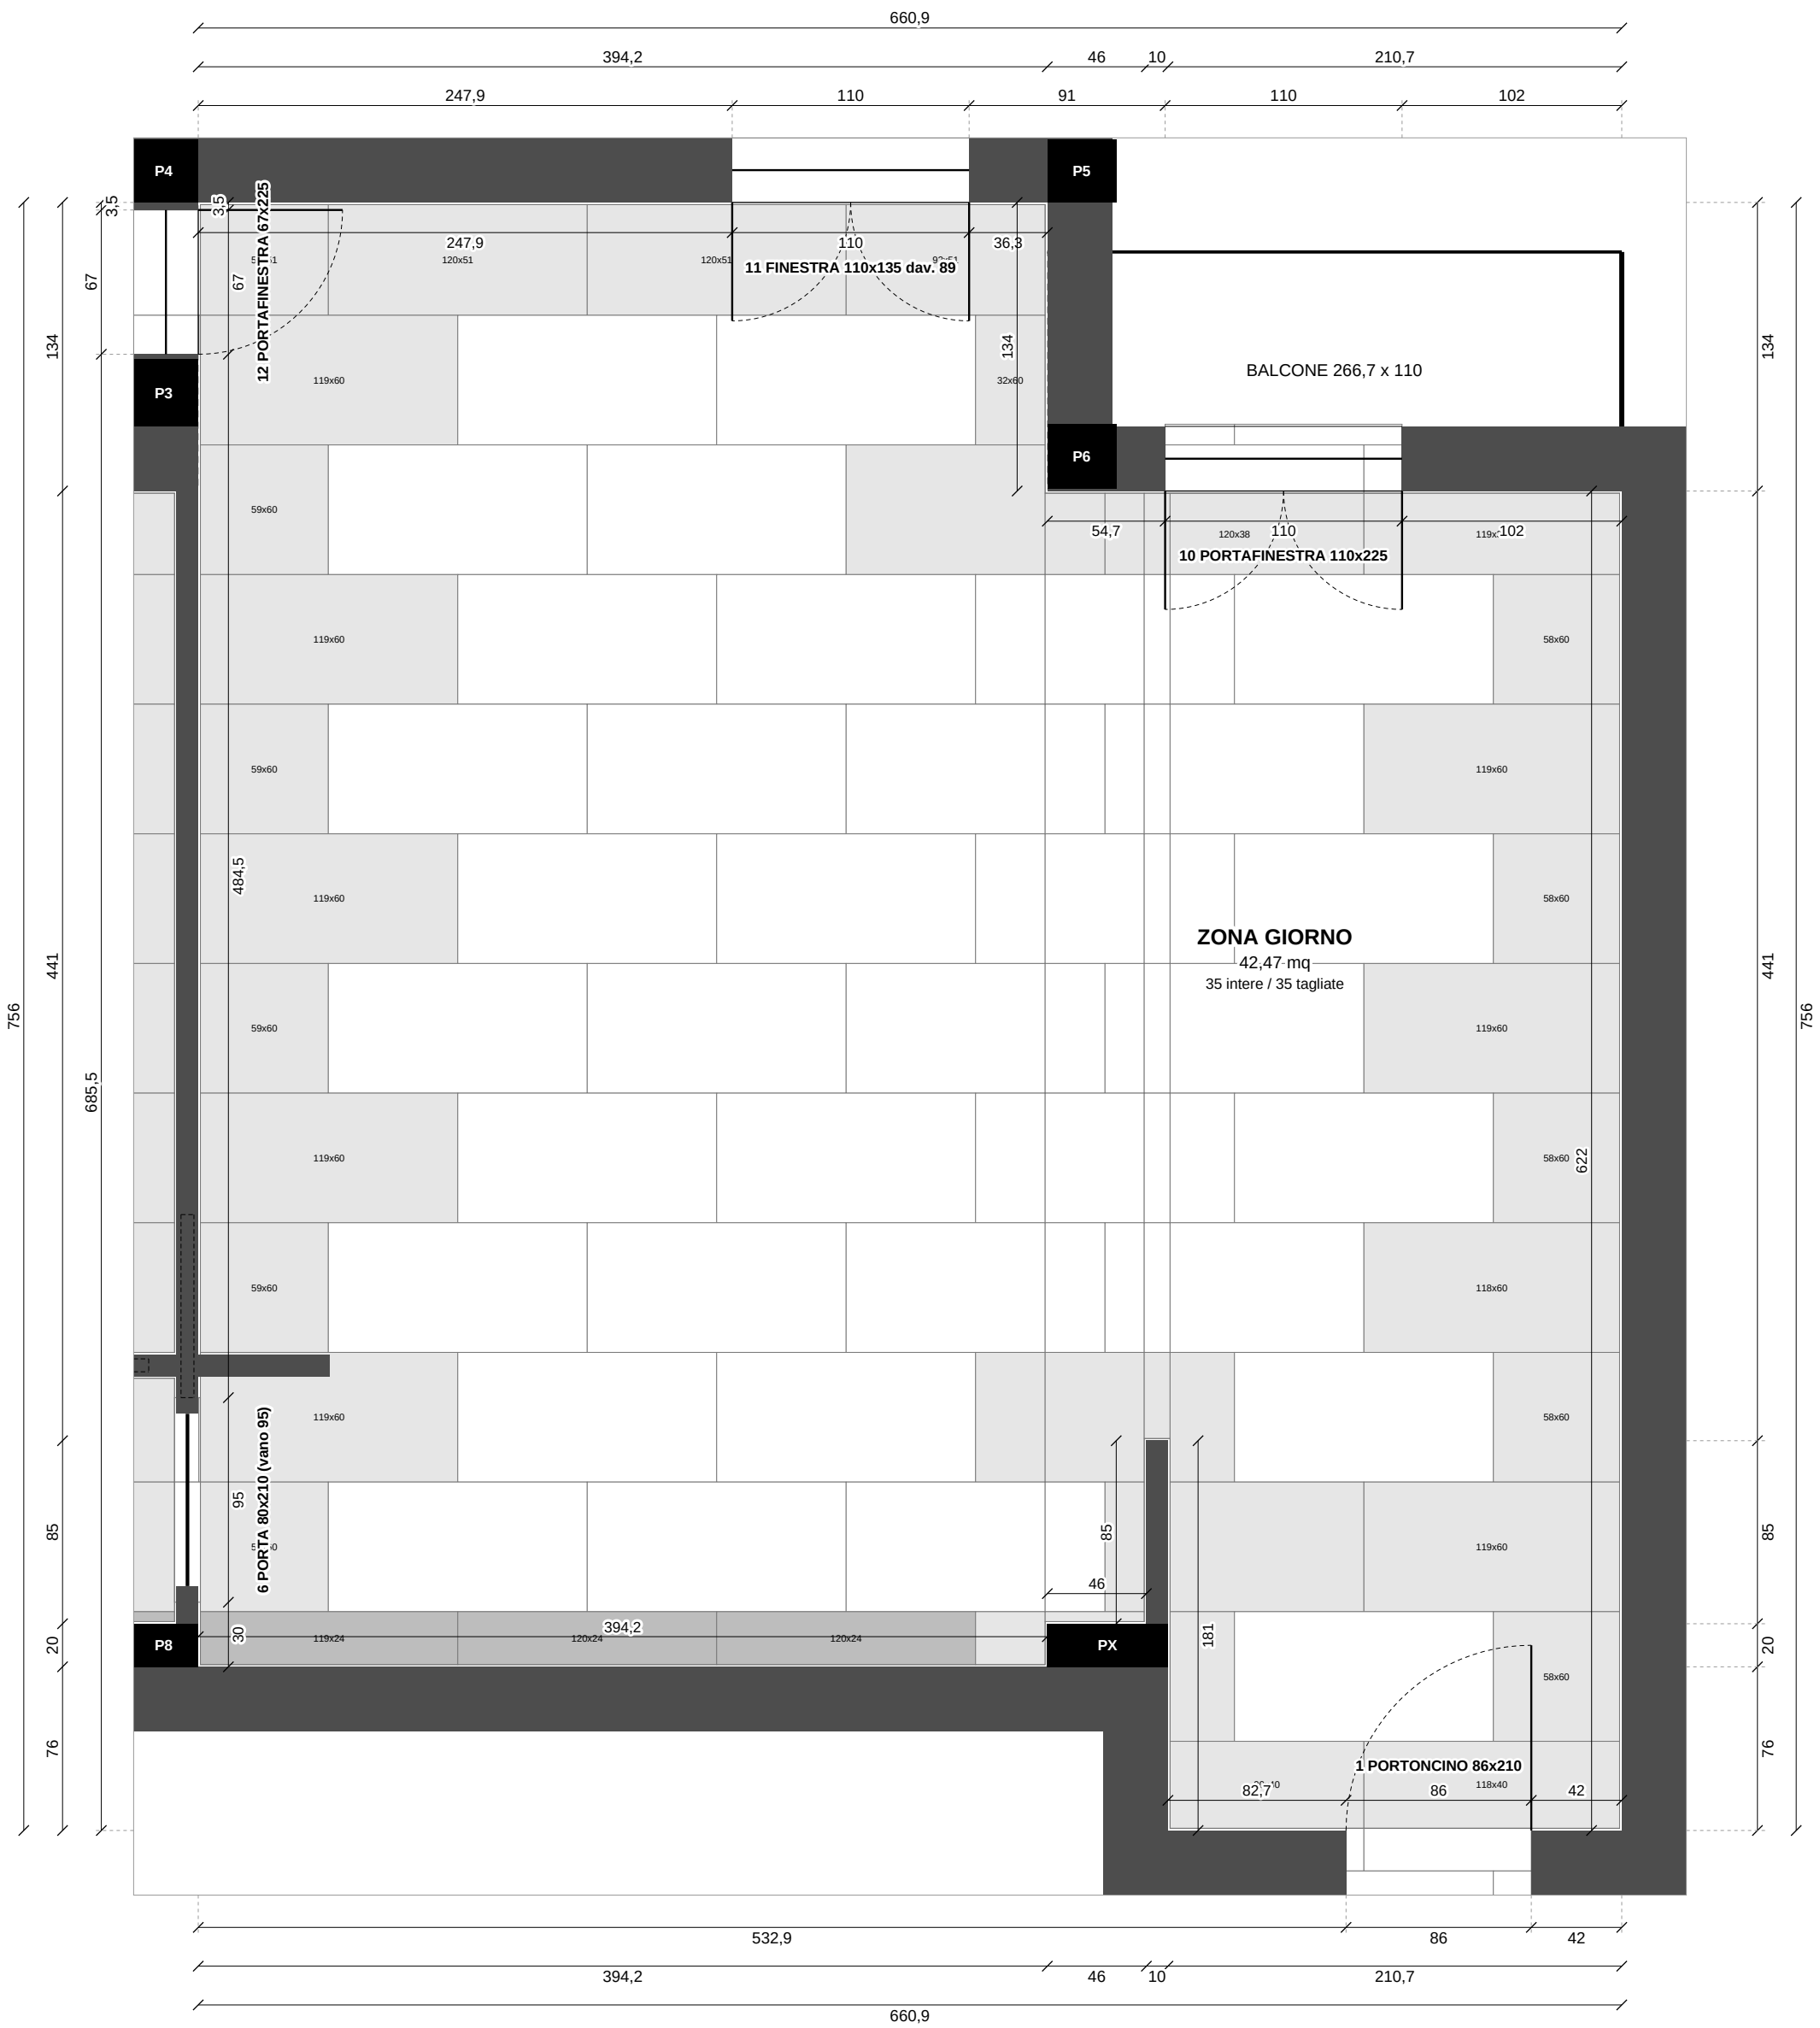

quote in cm al filo muro (prima di rivestimento e battiscopa); dentro i locali le misure di ogni lato con le aperture, fuori le catene di facciata; porte a scomparsa con tasca tratteggiata; nei pezzi tagliati la misura della lastra (x per y)

ZONA NOTTE - camere, bagno, disimpegno, ripostiglio - scala 1:30 (A3)

Posa pavimento #5 (ordine di sfrido del modello 3D): gres 120x60, sfalsata 1/2, fuga 2 mm, origine griglia 29,1 / 53,6 - 134 lastre (96,5 mq), 57 intere, 101 tagliate, sfrido 13,6%

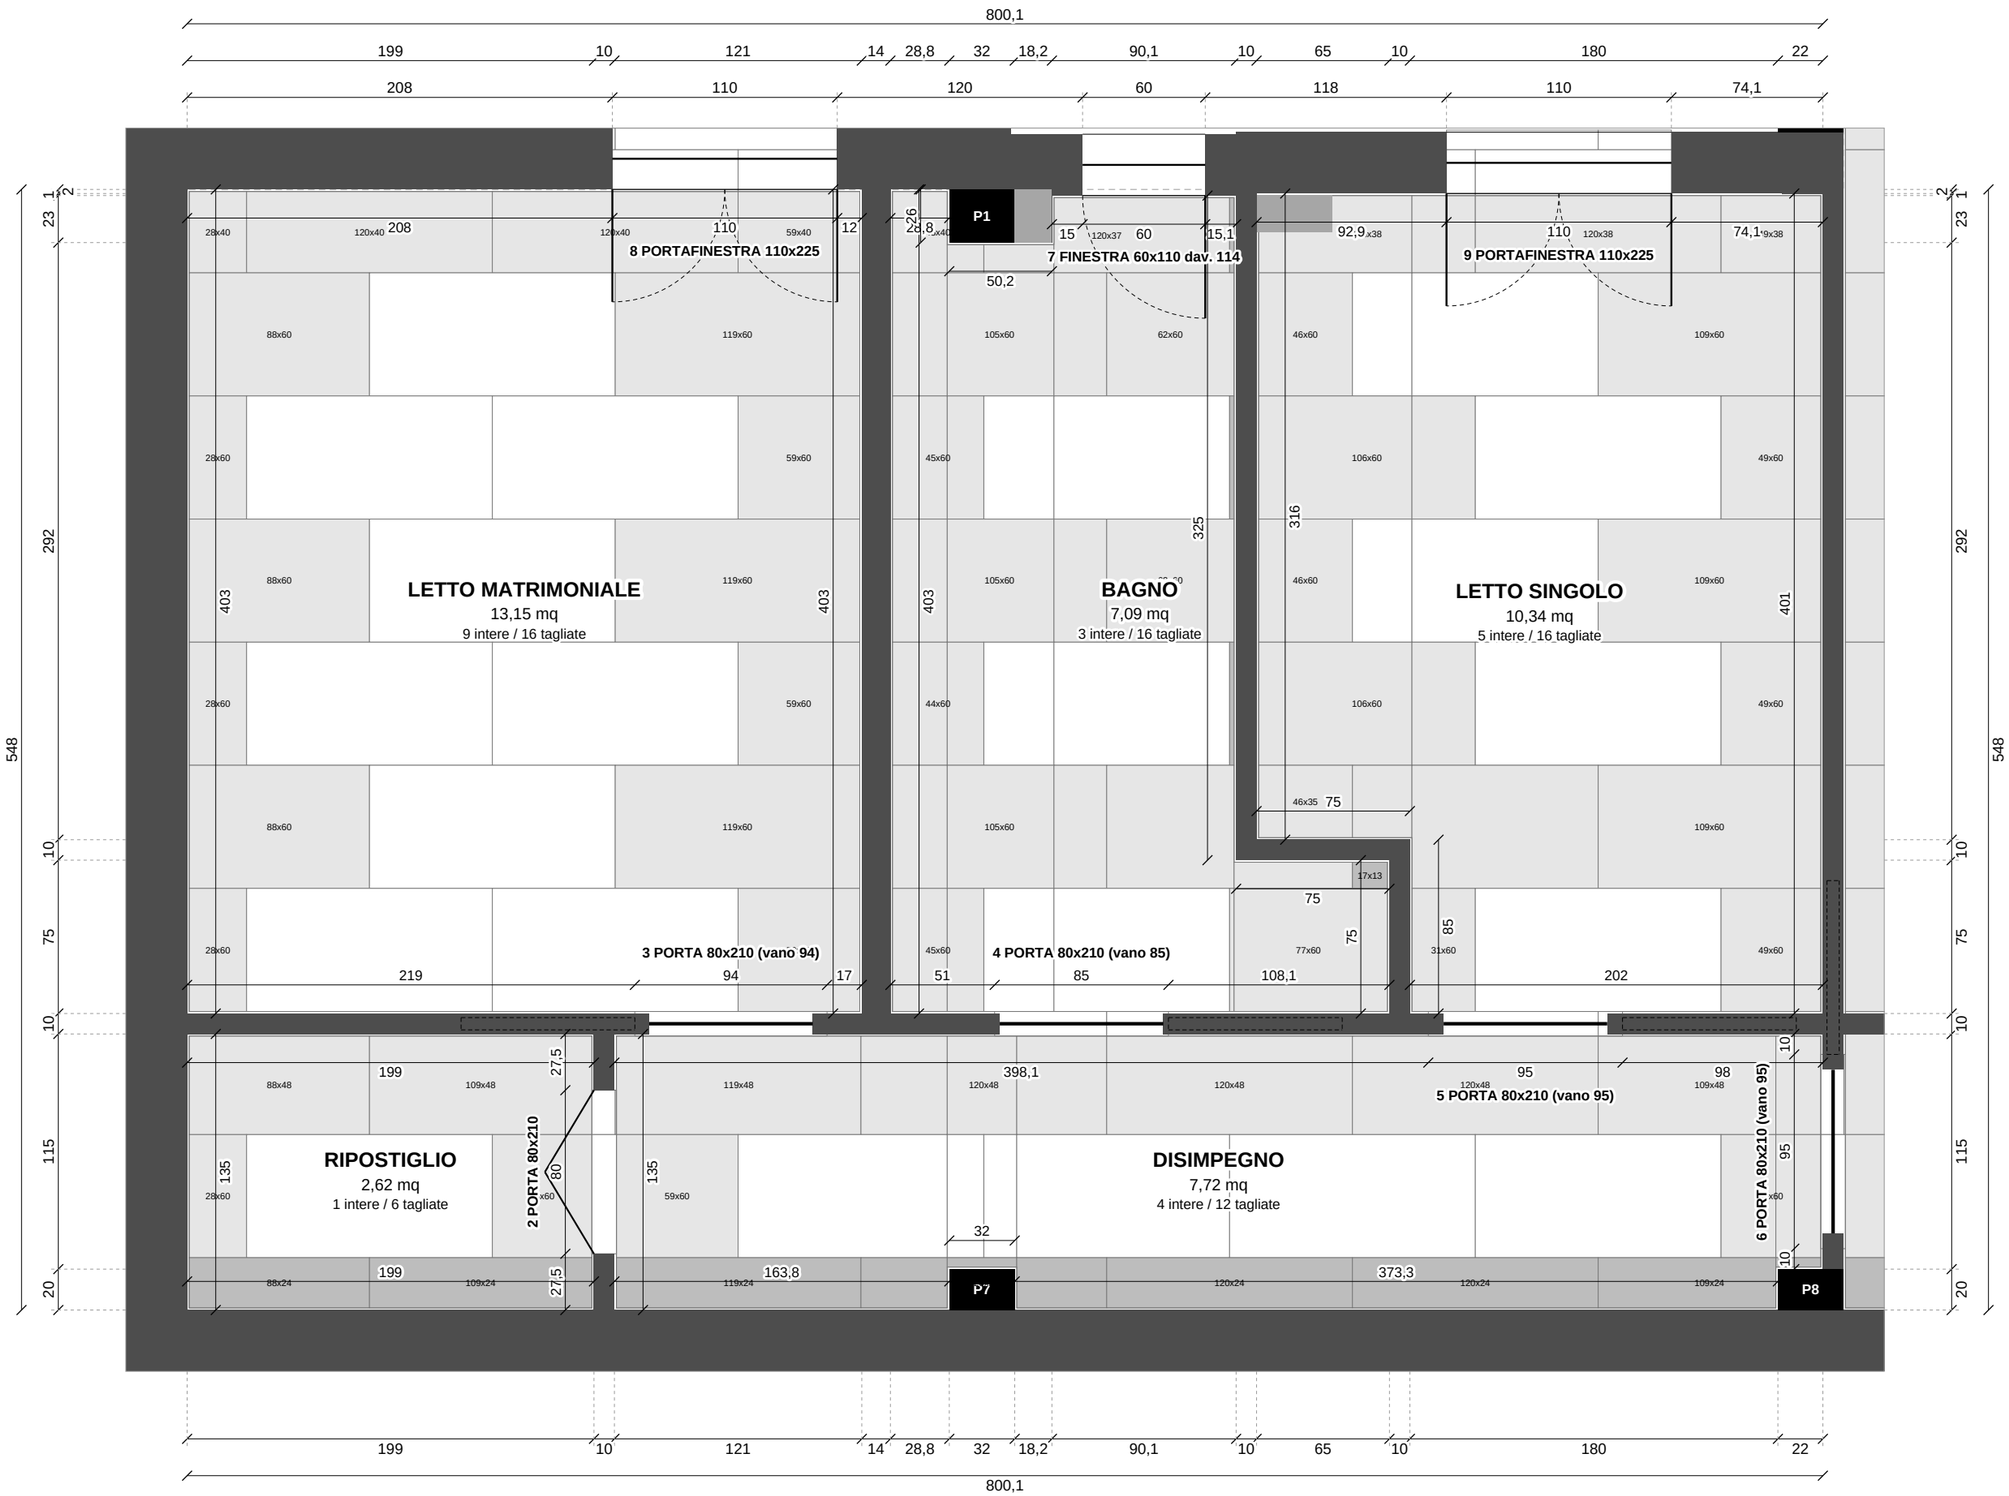

0 1 2 3 m

lastra intera 120x60 · lastra tagliata · listello, lato < 25 cm · muri sezionati a 150 cm · pilastri in c.a.

quote in cm al filo muro (prima di rivestimento e battiscopa); dentro i locali le misure di ogni lato con le aperture, fuori le catene di facciata; porte a scomparsa con tasca tratteggiata; nei pezzi tagliati la misura della lastra (x per y)