


BAGNO - pianta di progetto

Vano finito 391 x 154 cm - 6.50 mq - perimetro 12.86 m - rivestimento interno 2 cm - piastrelle 90x90

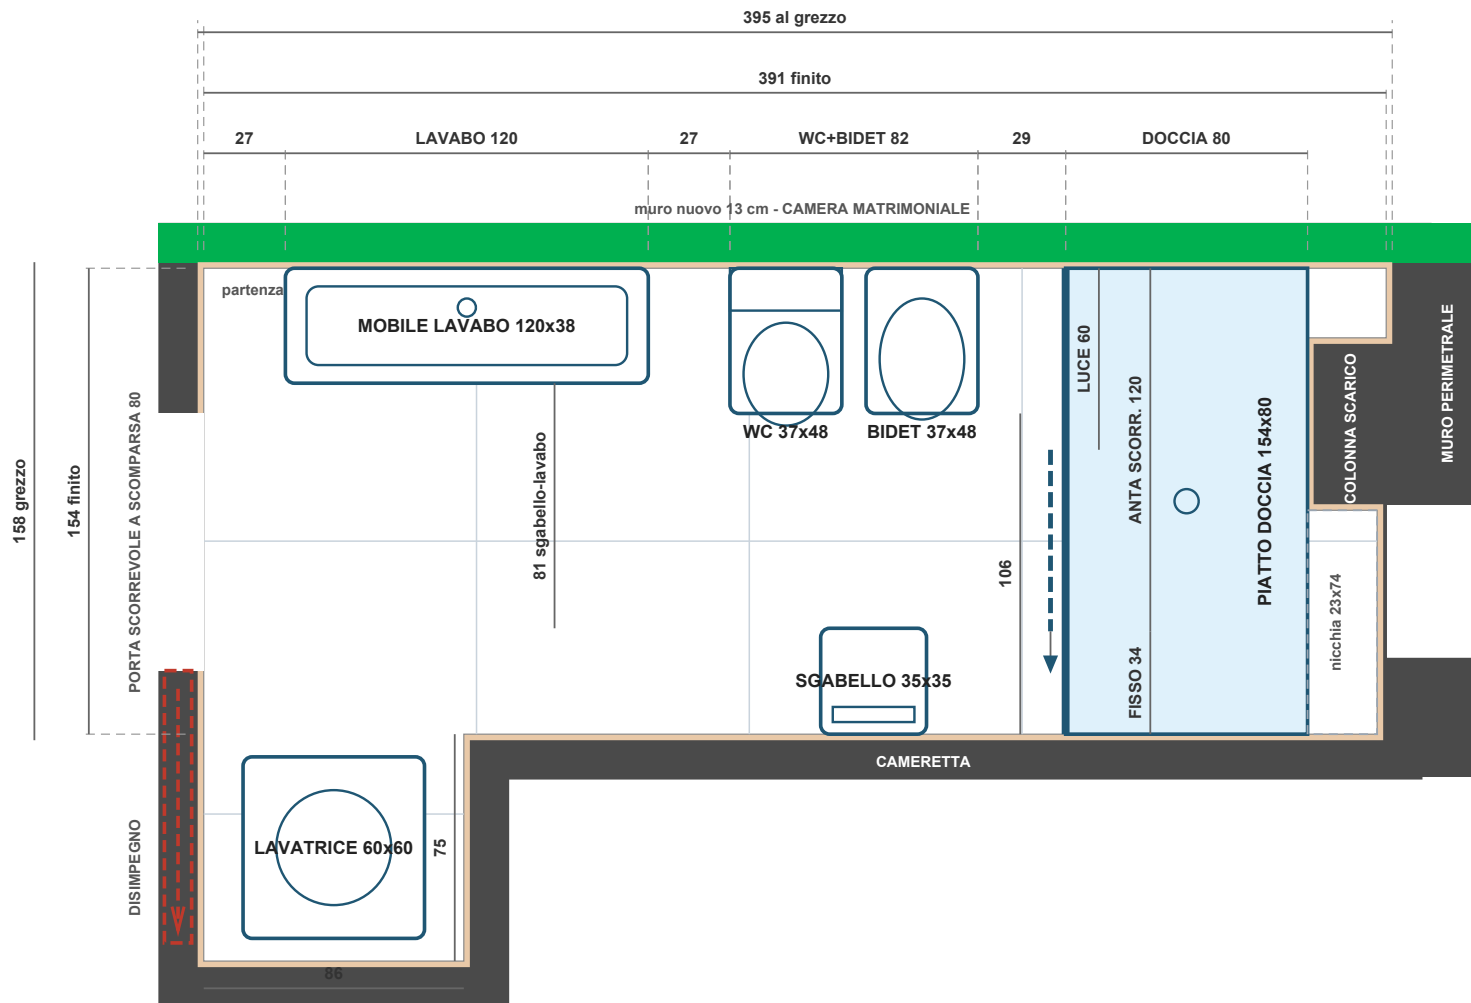

PIASTRELLE 90x90
lastra: 0.81 mq - fuga 2 mm
PAVIMENTO 6.50 mq
file intere: 4 x 2
taglio in fondo: 30 cm
taglio lato cameretta: 64 cm
taglio fondo nicchia: 49 cm
lastre (+15%): 10
RIVESTIMENTO h 240 cm
12.86 m x 2.40 m - vuoti
= 28.73 mq
3 corsi da 80, l'ultimo tagliato
spessore in opera: 2 cm
lastre (+15%): 41
TOTALE 51 lastre = 41.3 mq

Rivestimento interno 2 cm (piastrella + colla) su tutte le pareti: misure FINITE 154 x 391 cm contro 158 x 395 al grezzo. Tutte le quote e l'arredo si riferiscono al finito.

Sanitari accentrati sul tratto libero 2-287: interasse wc-bidet 45 cm, luce laterale 27 cm. Wc e bidet sospesi, profondi 48. Passaggio libero 106 cm per tutto il vano.

Box a nicchia 154: anta scorrevole a 2 pannelli, 120 da chiusa e 60 da aperta, + fisso 34. Luce netta di accesso alla doccia 60 cm.

Piatto doccia 154x80 su misura a filo colonna di scarico; nicchia 23x74 sotto la finestra da tamponare (seduta h 45). Porta 80x210 a scomparsa: parete finita min. 12,5 cm.

Colonna montante di scarico nell'angolo di fondo, dietro al piatto: dal wc lo scarico corre ~2 m sotto pavimento (verificare pendenza e massetto).

scala 1:25 alla stampa 100%

