


APPARTAMENTO - posa gres 60x60

origine di posa ottimale 1.0 / 2.1 cm - minimo numero di lastre e di tagli; rivestimento bagno su 5 corsi a filo trave
fuga 1.5 mm - modulo 60.15 cm - griglia unica continua su tutta la casa - battiscopa/rivestimento 1 cm - origine 1.0/2.1 - stampa 100% = 1:60

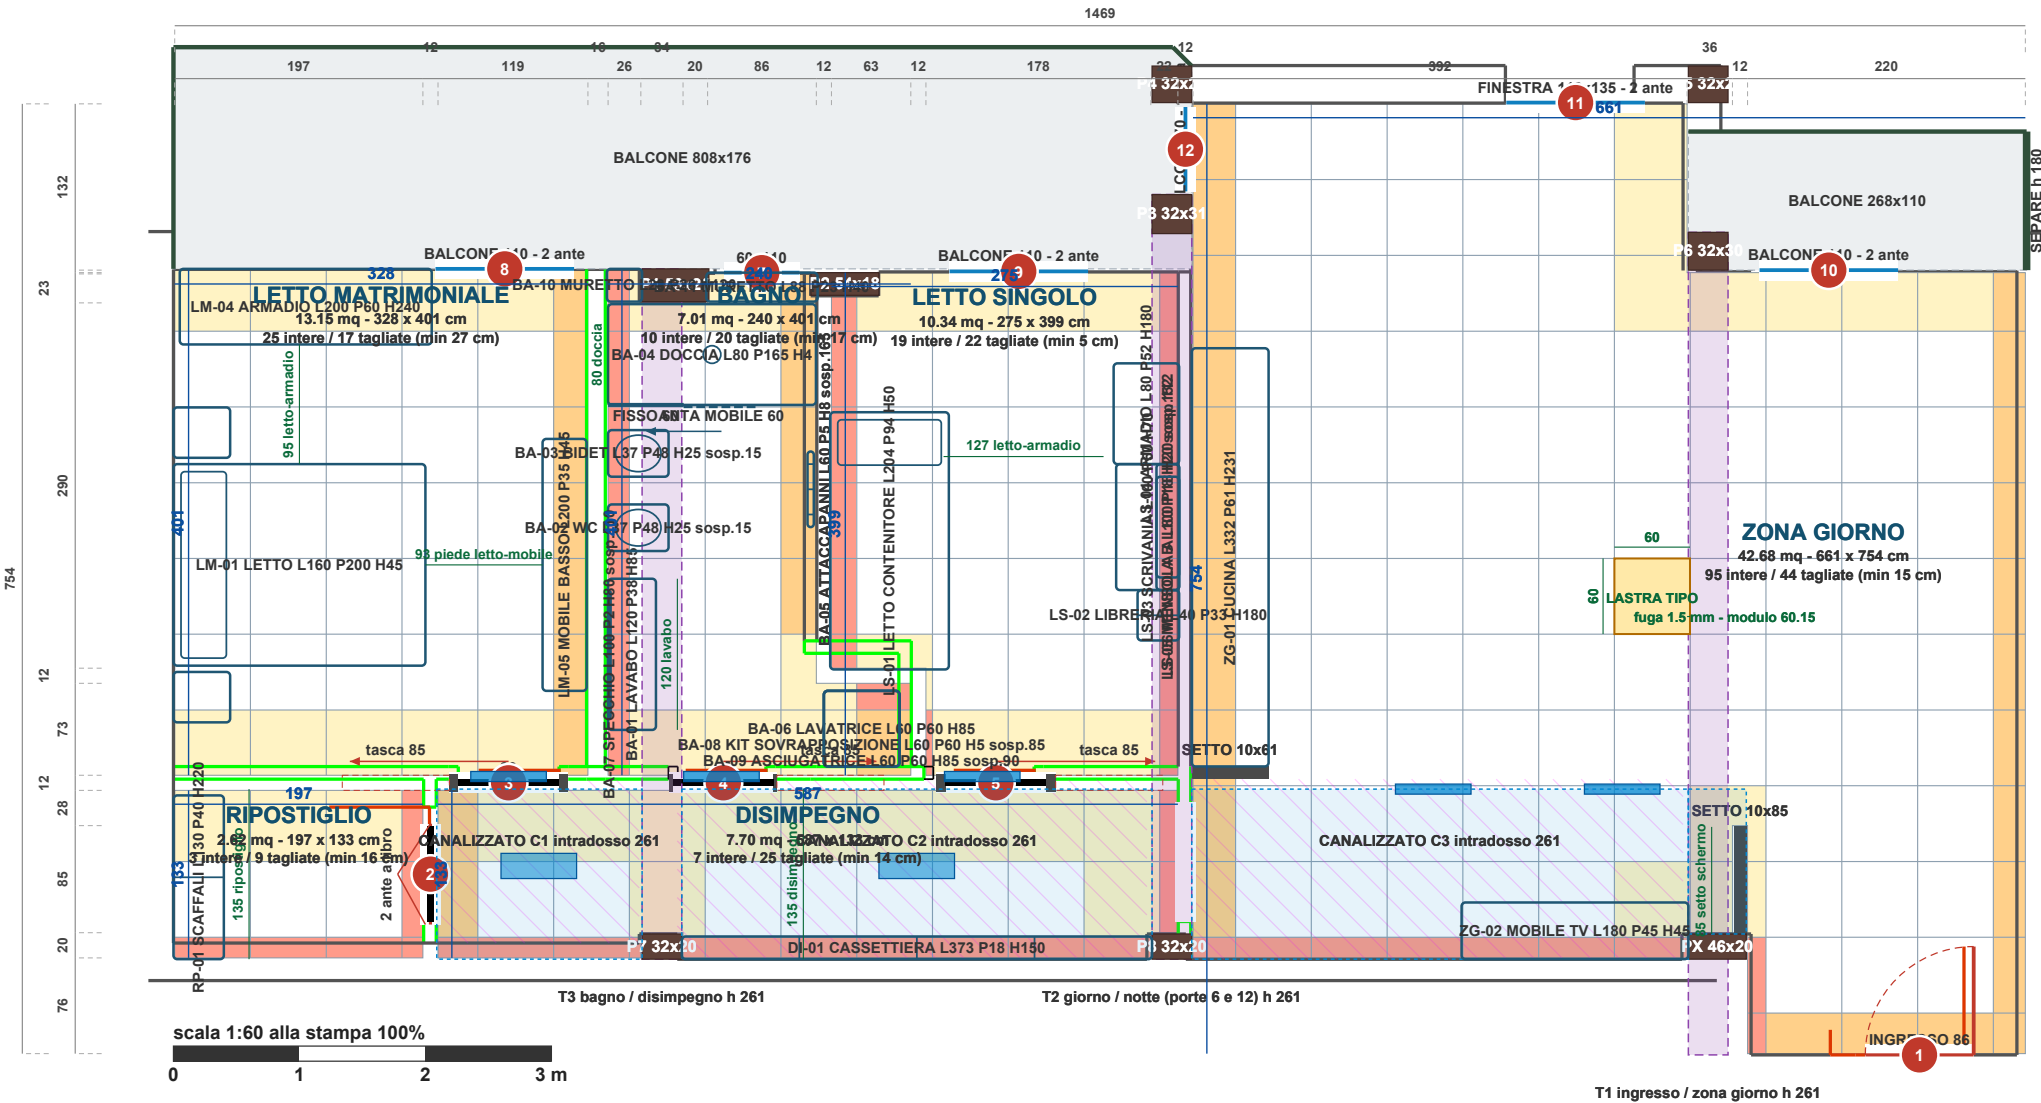

LEGENDA LASTRE

- intera 60x60
- tagliata, lato >= 45 cm (taglio buono)
- tagliata, lato 25-45 cm
- tagliata, lato < 25 cm (listello: da evitare)

CONFRONTO FORMATI (ognuno con la sua origine di posa ottimale)

formato	origine X/Y	lastre intere	tagliate	tagli < 25 cm	tagli 25-45	tagli > 45	lato minimo	% sup. con intere	lastre / sfrido
90x90, 3 corsi a filo trave	63.4 / 24.2	49	88	7	19	62	13 cm	48%	124 / 17%
80x80, 4 corsi a filo trave	37.7 / 59.0	77	97	18	29	50	1 cm	59%	152 / 14%
60x60, 5 corsi a filo trave	1.0 / 2.1	159	137	49	40	48	5 cm	69%	261 / 11%