


APPARTAMENTO - posa gres 80x80

origine di posa ottimale 37.7 / 59.0 cm - minimo numero di lastre e di tagli; rivestimento bagno su 4 corsi a filo trave  
fuga 1.5 mm - modulo 80.15 cm - griglia unica continua su tutta la casa - battiscopa/rivestimento 1 cm - origine 37.7/59.0 - stampa 100% = 1:60

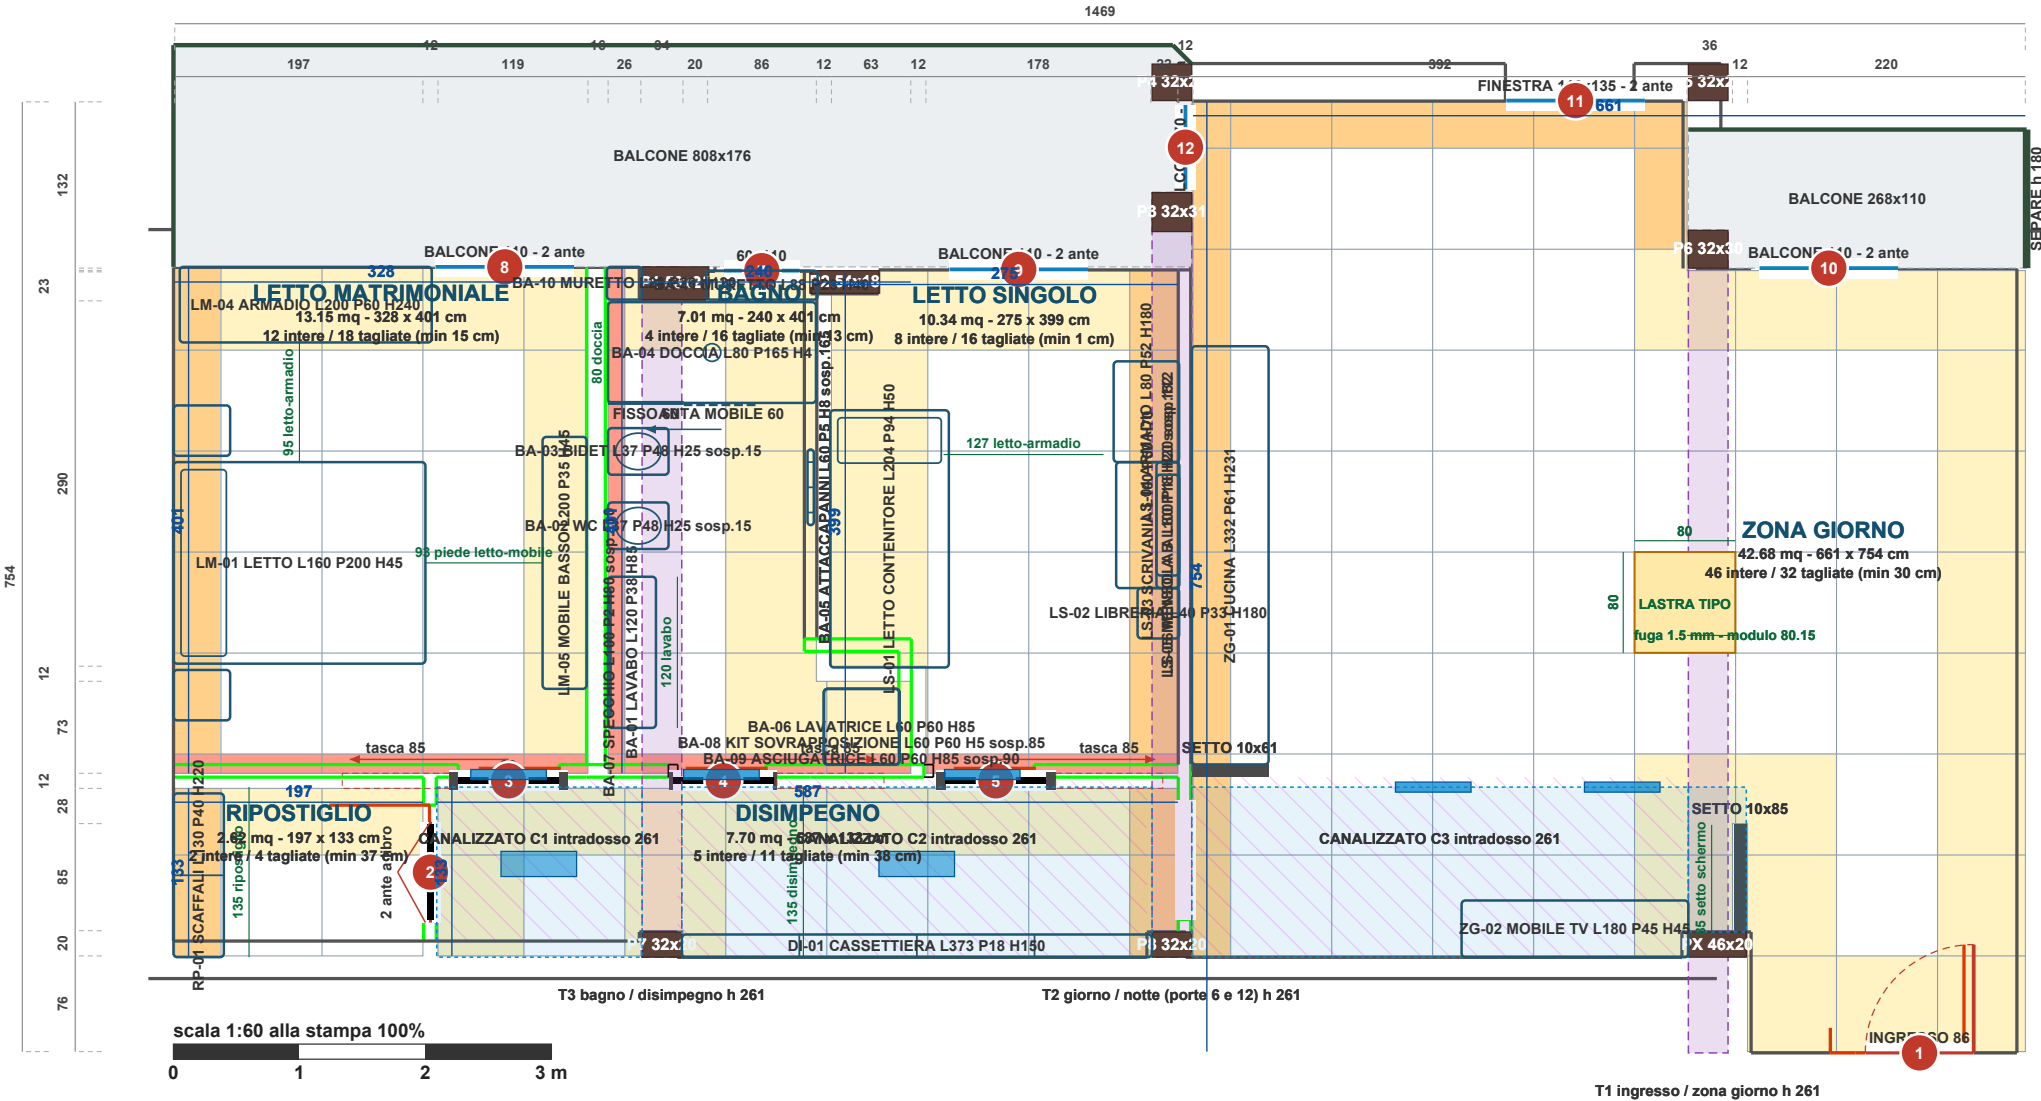

LEGENDA LASTRE

- intera 80x80
- tagliata, lato >= 45 cm (taglio buono)
- tagliata, lato 25-45 cm
- tagliata, lato < 25 cm (listello: da evitare)

| CONFRONTO FORMATI (ognuno con la sua origine di posa ottimale) |             |               |          |               |             |            |             |                   |                 |
|----------------------------------------------------------------|-------------|---------------|----------|---------------|-------------|------------|-------------|-------------------|-----------------|
| formato                                                        | origine X/Y | lastre intere | tagliate | tagli < 25 cm | tagli 25-45 | tagli > 45 | lato minimo | % sup. con intere | lastre / sfrido |
| 90x90, 3 corsi a filo trave                                    | 63.4 / 24.2 | 49            | 88       | 7             | 19          | 62         | 13 cm       | 48%               | 124 / 17%       |
| 80x80, 4 corsi a filo trave                                    | 37.7 / 59.0 | 77            | 97       | 18            | 29          | 50         | 1 cm        | 59%               | 152 / 14%       |
| 60x60, 5 corsi a filo trave                                    | 1.0 / 2.1   | 159           | 137      | 49            | 40          | 48         | 5 cm        | 69%               | 261 / 11%       |