


MURO-SCHERMO ALL'INGRESSO - copertura visiva del fronte cucina

Prolungamento verso l'alto della spalla sinistra del vano d'ingresso (X=1248,5). Visuale calcolata dal punto piu' sfavorevole del vano porta.

Fronte cucina 360 cm - stampa 100% = 1:30

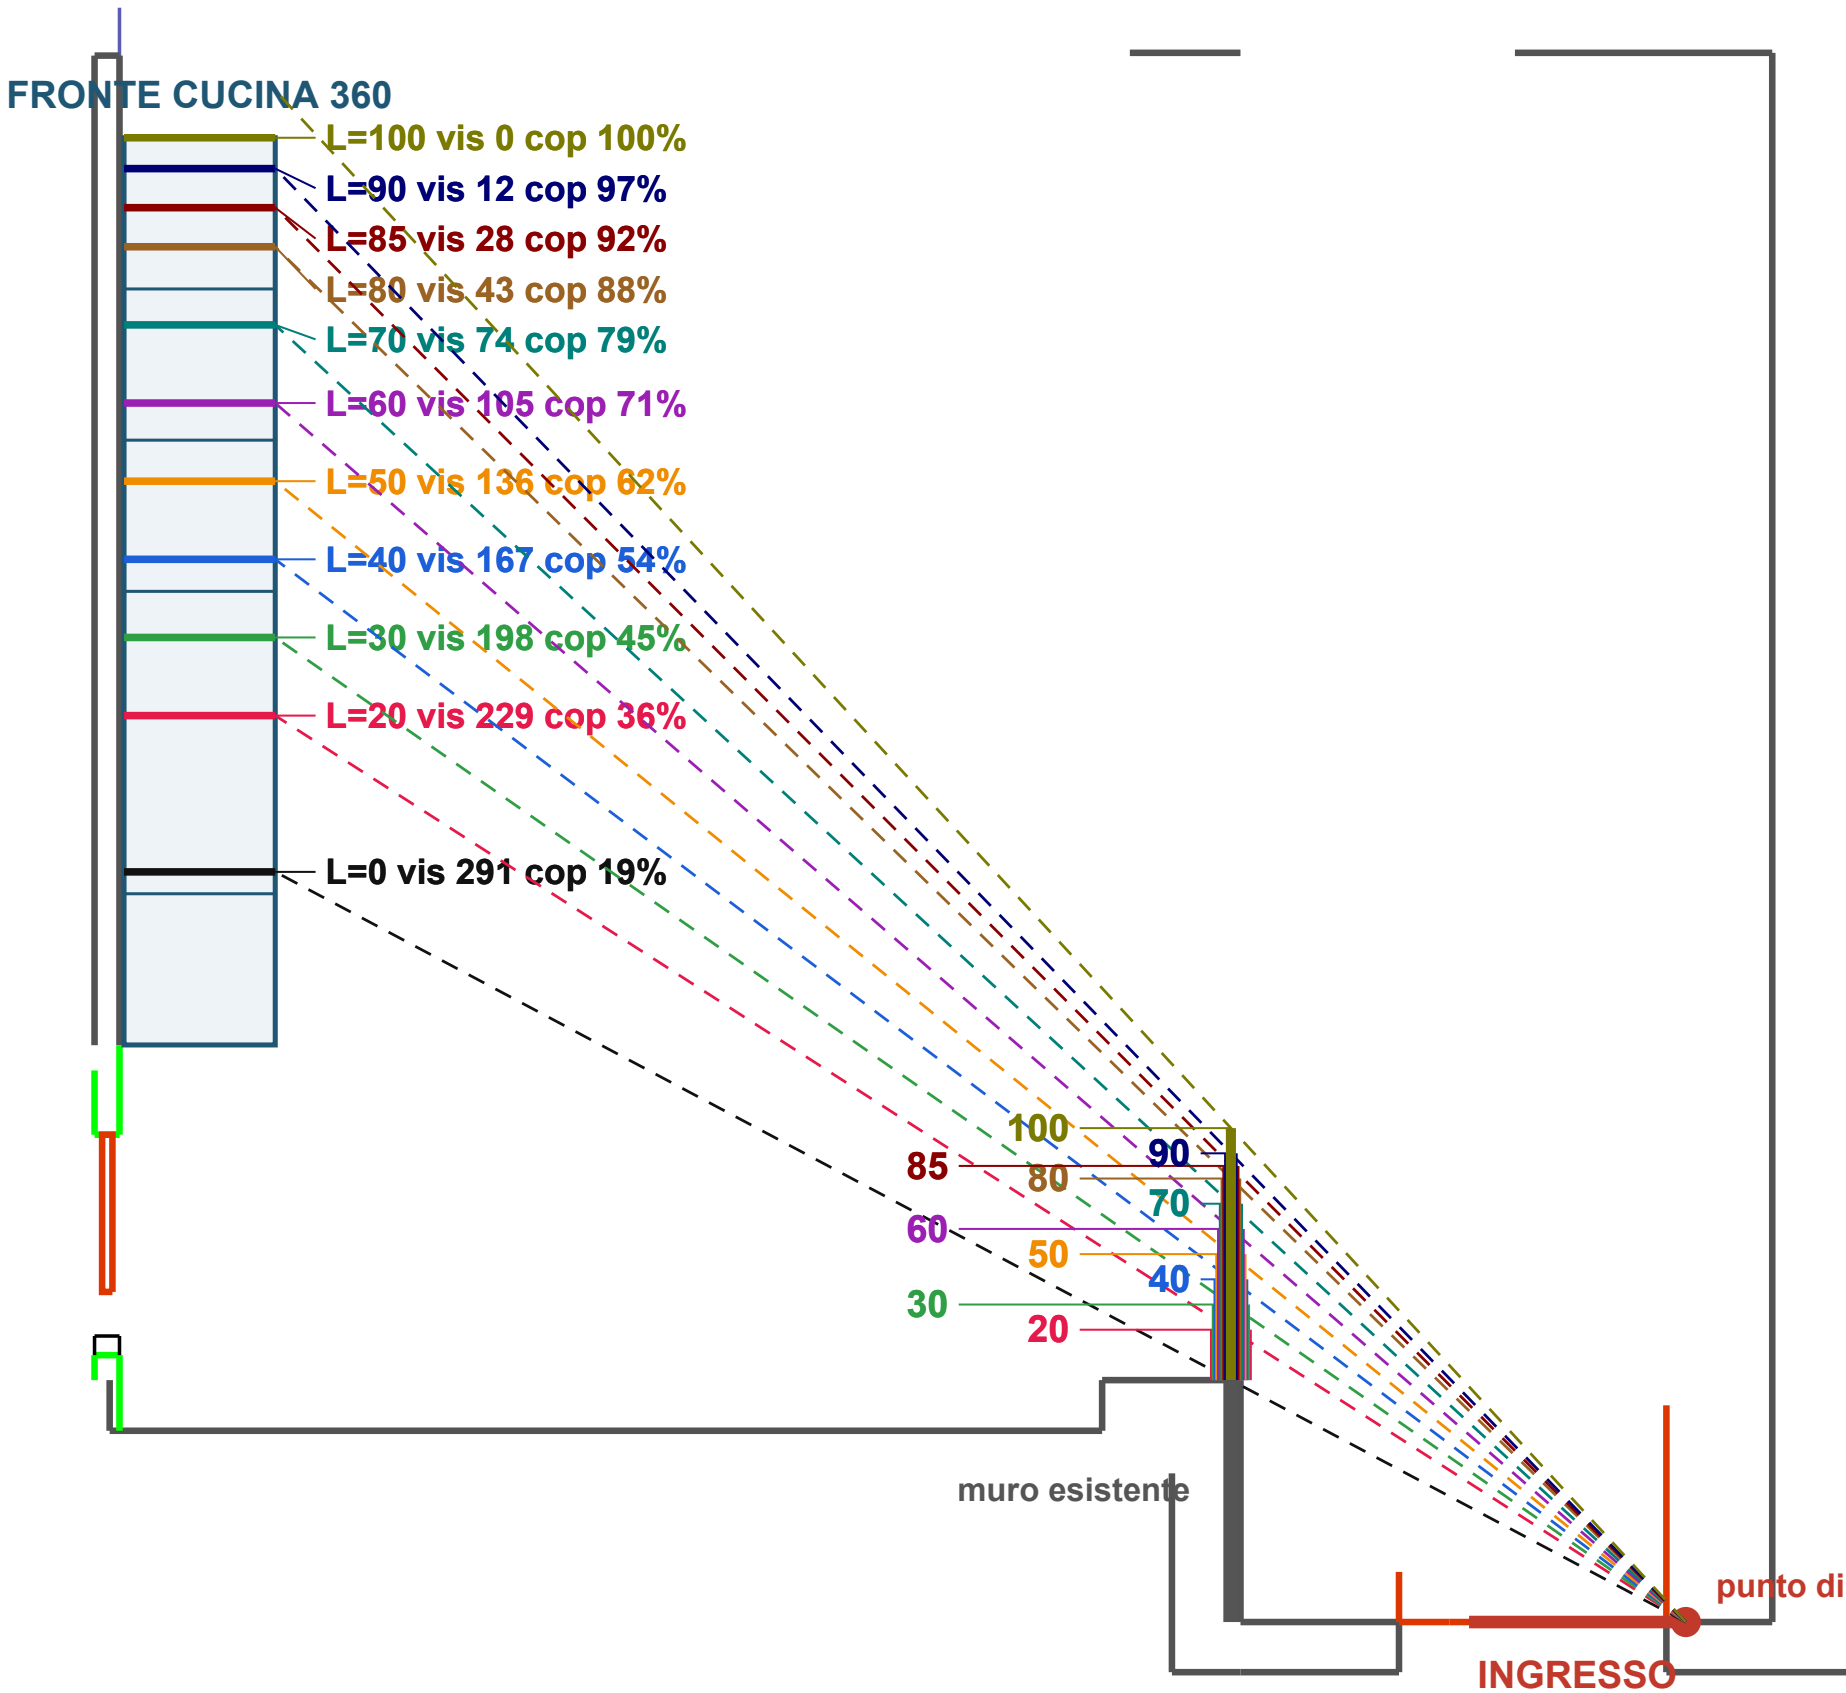

LUNGHEZZE A CONFRONTO

	L = 0 cm	visibile 291 cm	coperto 19%
	L = 20 cm	visibile 229 cm	coperto 36%
	L = 30 cm	visibile 198 cm	coperto 45%
	L = 40 cm	visibile 167 cm	coperto 54%
	L = 50 cm	visibile 136 cm	coperto 62%
	L = 60 cm	visibile 105 cm	coperto 71%
	L = 70 cm	visibile 74 cm	coperto 79%
	L = 80 cm	visibile 43 cm	coperto 88%
	L = 85 cm	visibile 28 cm	coperto 92%
	L = 90 cm	visibile 12 cm	coperto 97%
	L = 100 cm	visibile 0 cm	coperto 100%

SOGLIE

meta' cucina -> muro 36 cm

3/4 di cucina -> muro 65 cm

cucina intera -> muro 94 cm

consigliato 90 cm: copre tutto e cade su una fuga del 90x90 (nessun taglio in piu')