


BAGNO - pianta di progetto

Vano finito 391 x 165 cm - 6.93 mq - perimetro 13.08 m - rivestimento interno 2 cm - piastrelle 90x90

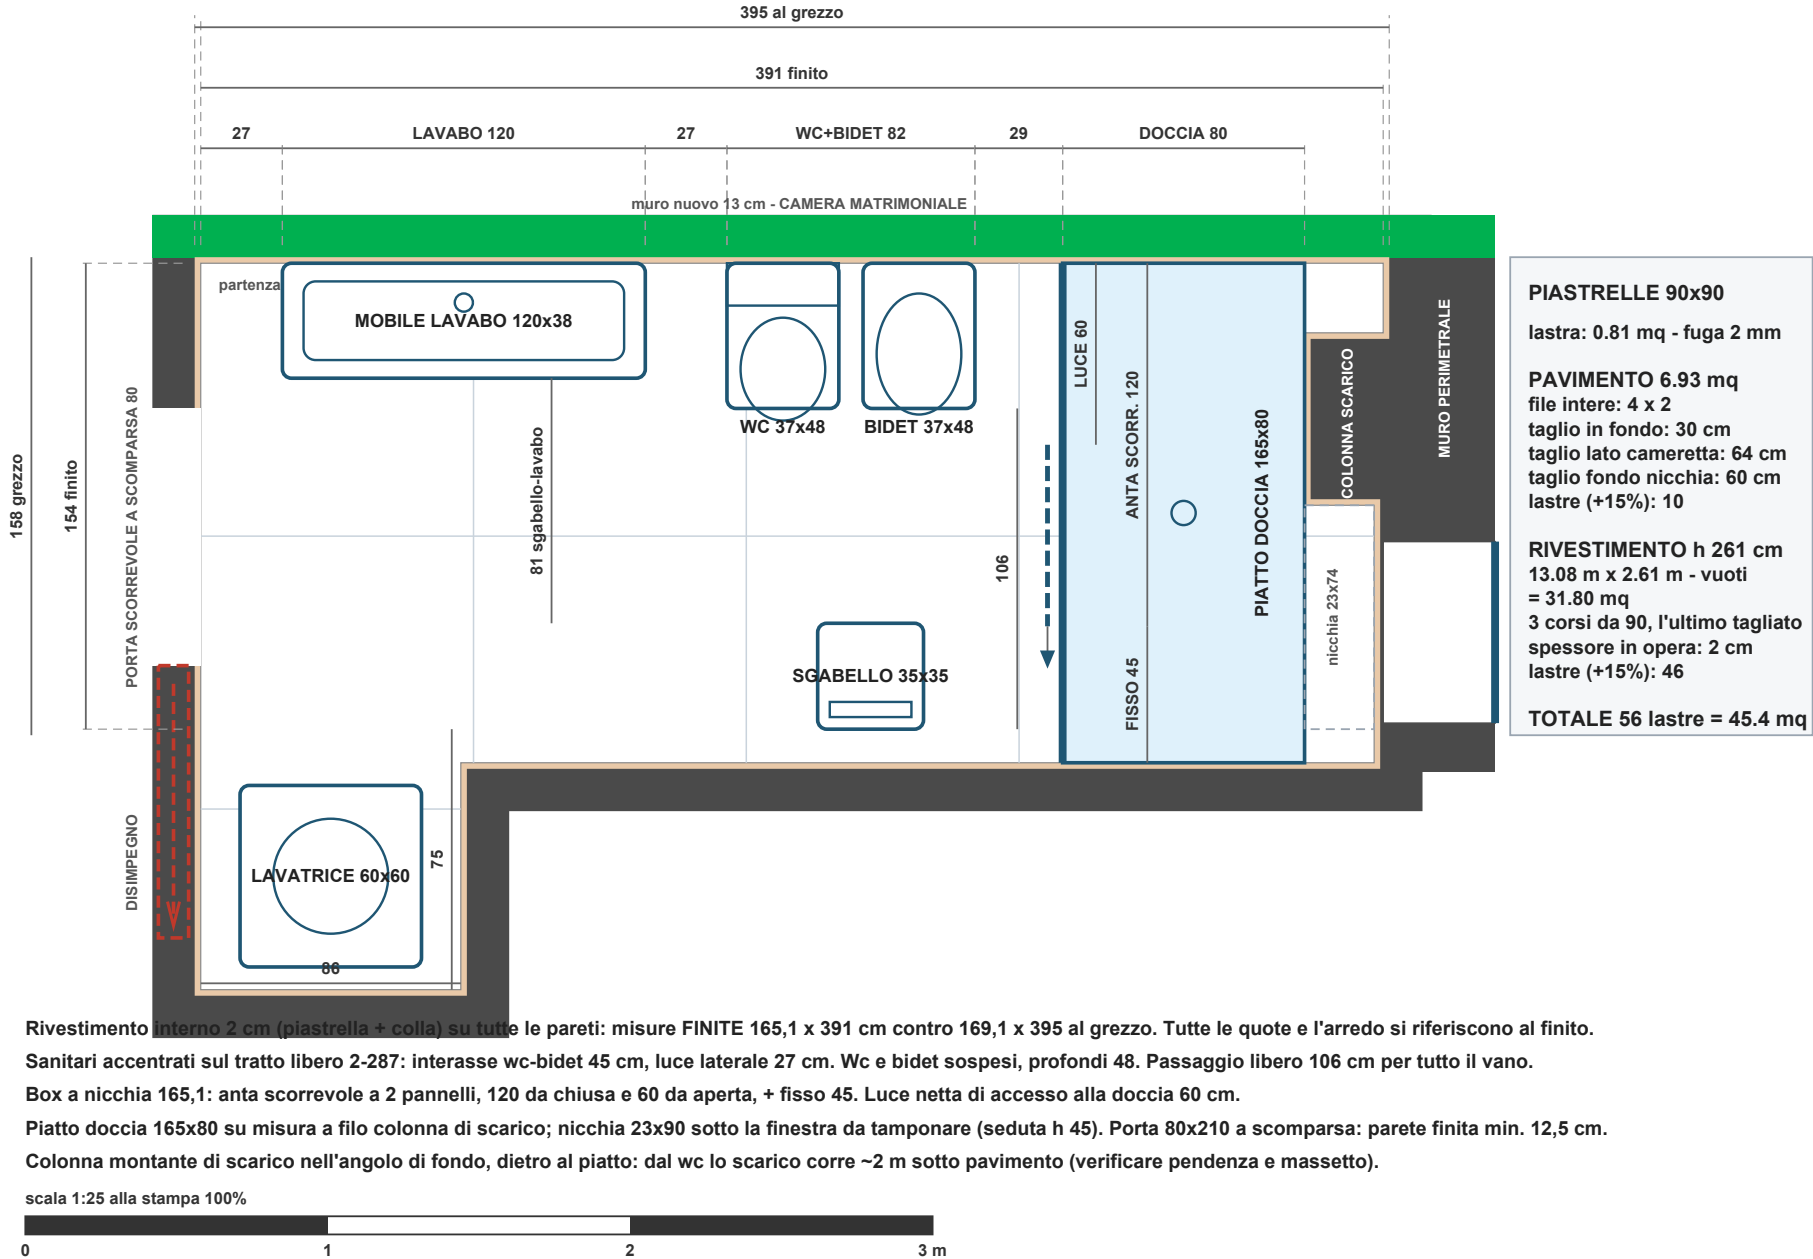

Rivestimento interno 2 cm (piastrella + colla) su tutte le pareti: misure FINITE 165,1 x 391 cm contro 169,1 x 395 al grezzo. Tutte le quote e l'arredo si riferiscono al finito.

Sanitari accentrati sul tratto libero 2-287: interasse wc-bidet 45 cm, luce laterale 27 cm. Wc e bidet sospesi, profondi 48. Passaggio libero 106 cm per tutto il vano.

Box a nicchia 165,1: anta scorrevole a 2 pannelli, 120 da chiusa e 60 da aperta, + fisso 45. Luce netta di accesso alla doccia 60 cm.

Piatto doccia 165x80 su misura a filo colonna di scarico; nicchia 23x90 sotto la finestra da tamponare (seduta h 45). Porta 80x210 a scomparsa: parete finita min. 12,5 cm.

Colonna montante di scarico nell'angolo di fondo, dietro al piatto: dal wc lo scarico corre ~2 m sotto pavimento (verificare pendenza e massetto).

scala 1:25 alla stampa 100%

