


APPARTAMENTO - posa gres 120x60, 4 corsi a 240

origine di posa ottimale 88.6 / 53.6 cm - minimo numero di lastre e di tagli; rivestimento bagno su 4 corsi a 240
fuga 2.0 mm - modulo 120.20 x 60.20 cm - griglia unica continua su tutta la casa - battiscopa/rivestimento 1 cm - origine 88.6/53.6 - stampa 100% = 1:60

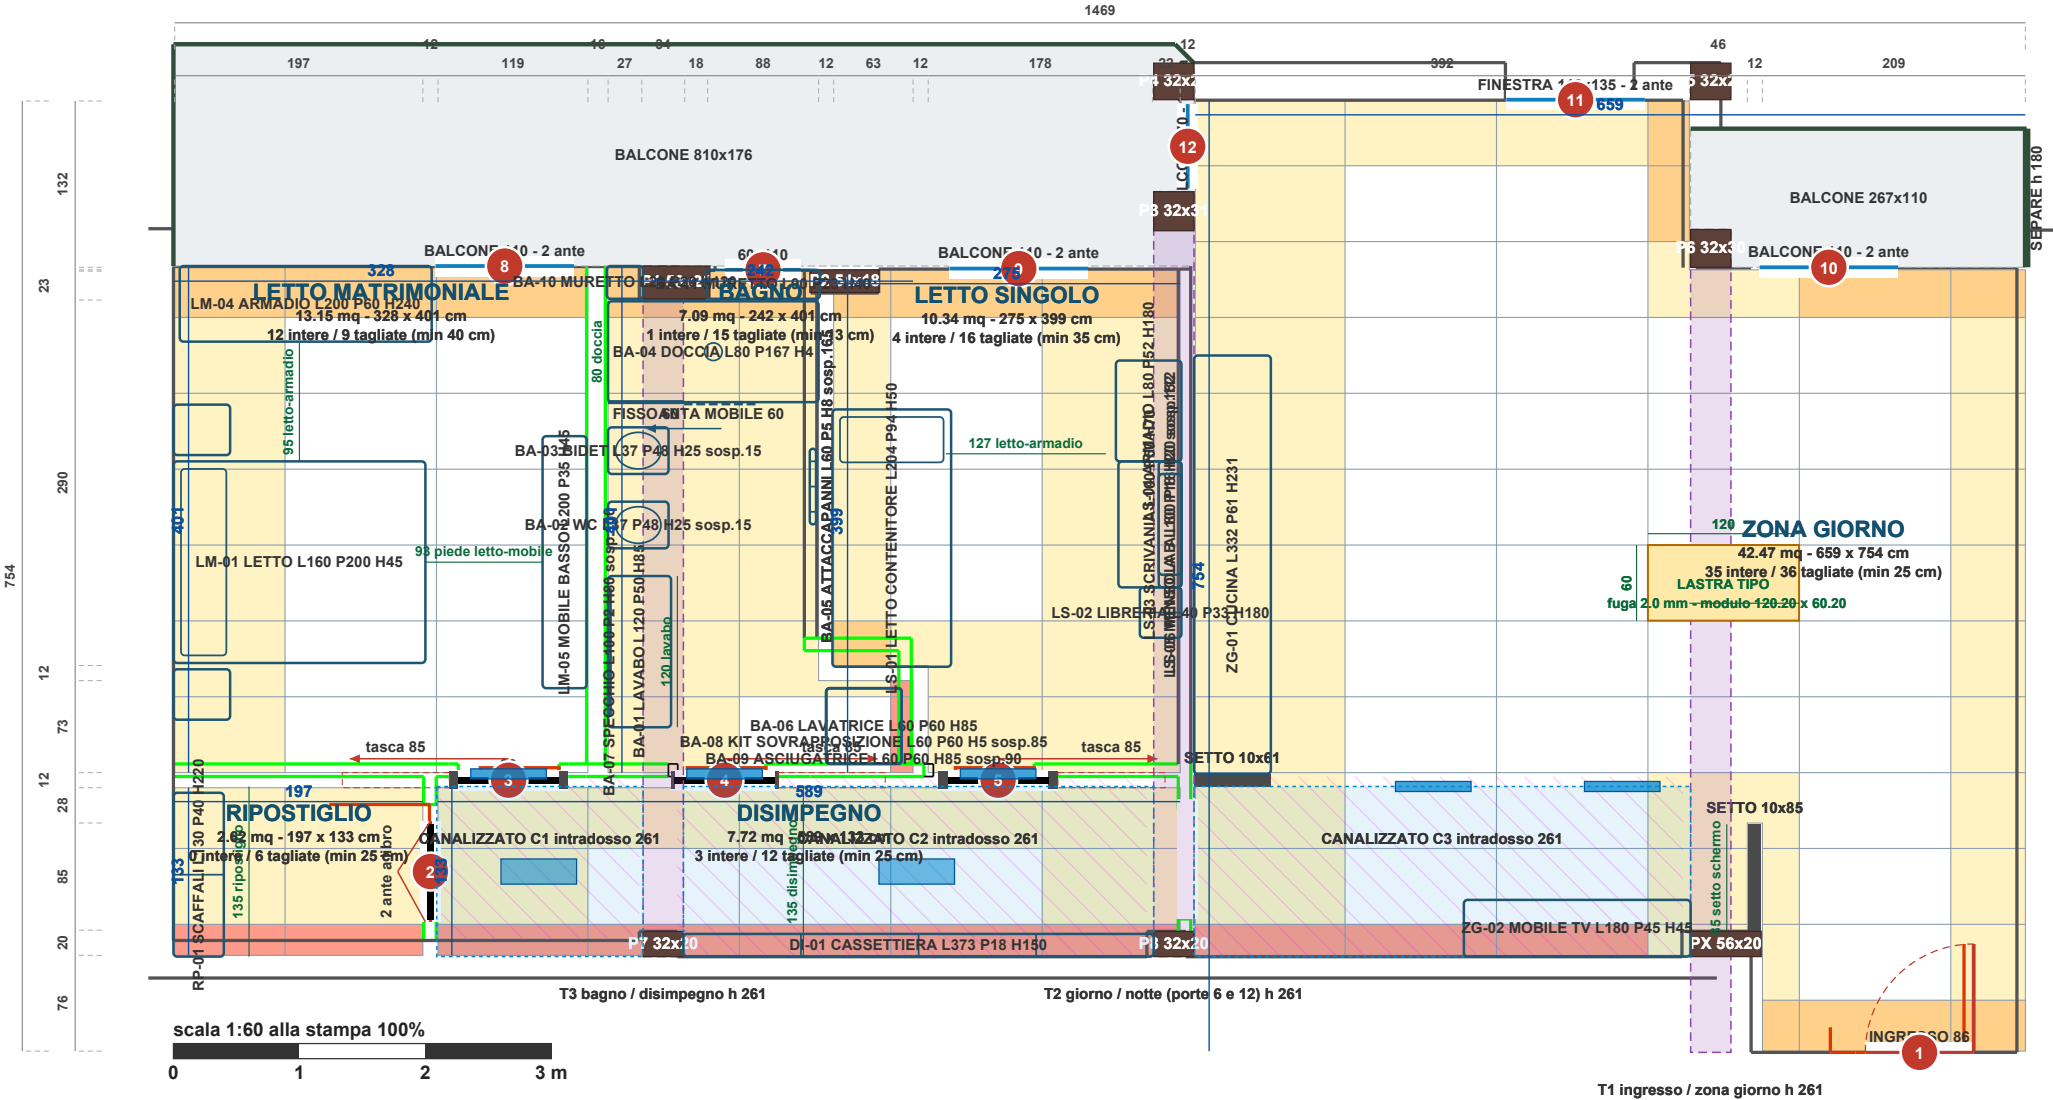

LEGENDA LASTRE

- intera 120x60
- tagliata, lato >= 45 cm (taglio buono)
- tagliata, lato 25-45 cm
- tagliata, lato < 25 cm (listello: da evitare)

CONFRONTO FORMATI (ognuno con la sua origine di posa ottimale)									
formato	origine X/Y	lastre intere	tagliate	tagli < 25 cm	tagli 25-45	tagli > 45	lato minimo	% sup. con intere	lastre / sfrido
90x90, 3 corsi a filo trave	26.8 / 24.0	63	83	3	45	35	4 cm	61%	123 / 16%
80x80, 4 corsi a filo trave	37.7 / 74.0	70	90	5	25	60	14 cm	54%	148 / 12%
60x60, 4 corsi a 240	28.5 / 53.6	155	121	28	40	53	2 cm	67%	259 / 11%
60x120, 2 corsi a 240	28.5 / 62.2	60	95	4	16	75	2 cm	52%	136 / 15%
60x120 pav 120x60 par, 4 corsi a 240	28.5 / 62.2	60	95	4	16	75	2 cm	52%	136 / 15%
120x60 pav 60x120 par, 2 corsi a 240	88.6 / 53.6	55	94	12	16	66	13 cm	47%	134 / 14%
120x60, 4 corsi a 240	88.6 / 53.6	55	94	12	16	66	13 cm	47%	134 / 14%
120x120, 2 corsi a 240, intera all'ingresso	118.3 / 95.0	31	76	23	29	24	3 cm	54%	82 / 29%
60x120, 2 corsi a 240, a filo bagno	30.5 / 6.2	71	97	32	58	7	1 cm	61%	142 / 18%
120x60, 4 corsi a 240, a filo bagno	31.3 / 5.4	63	103	18	73	3	3 cm	54%	139 / 17%
120x60, 4 corsi a 240, per stanza	27.6 / 33.8	82	68	11	18	39	12 cm	70%	134 / 13%
60x120, 2 corsi a 240, per stanza	28.5 / 62.2	84	73	20	24	29	11 cm	72%	137 / 15%
120x60, 4 corsi a 240, sfalsata 1/2	29.1 / 53.6	57	101	14	23	64	2 cm	49%	134 / 14%
120x60, 4 corsi a 240, sfalsata 1/3	117.9 / 53.6	60	101	18	29	54	11 cm	52%	141 / 18%
60x120, 2 corsi a 240, sfalsata 1/2	28.5 / 56.7	59	99	14	19	66	2 cm	51%	136 / 15%
60x120, 2 corsi a 240, sfalsata 1/3	28.5 / 102.3	62	100	13	28	59	2 cm	54%	142 / 18%