


APPARTAMENTO - posa gres 80x80 | variante A

A - minimo consumo: meno lastre e meno tagli in tutta la casa
fuga 1.5 mm - modulo 80.15 cm - griglia unica continua su tutta la casa - battiscopa/rivestimento 1 cm - origine 19.3/59.0 - stampa 100% = 1:60

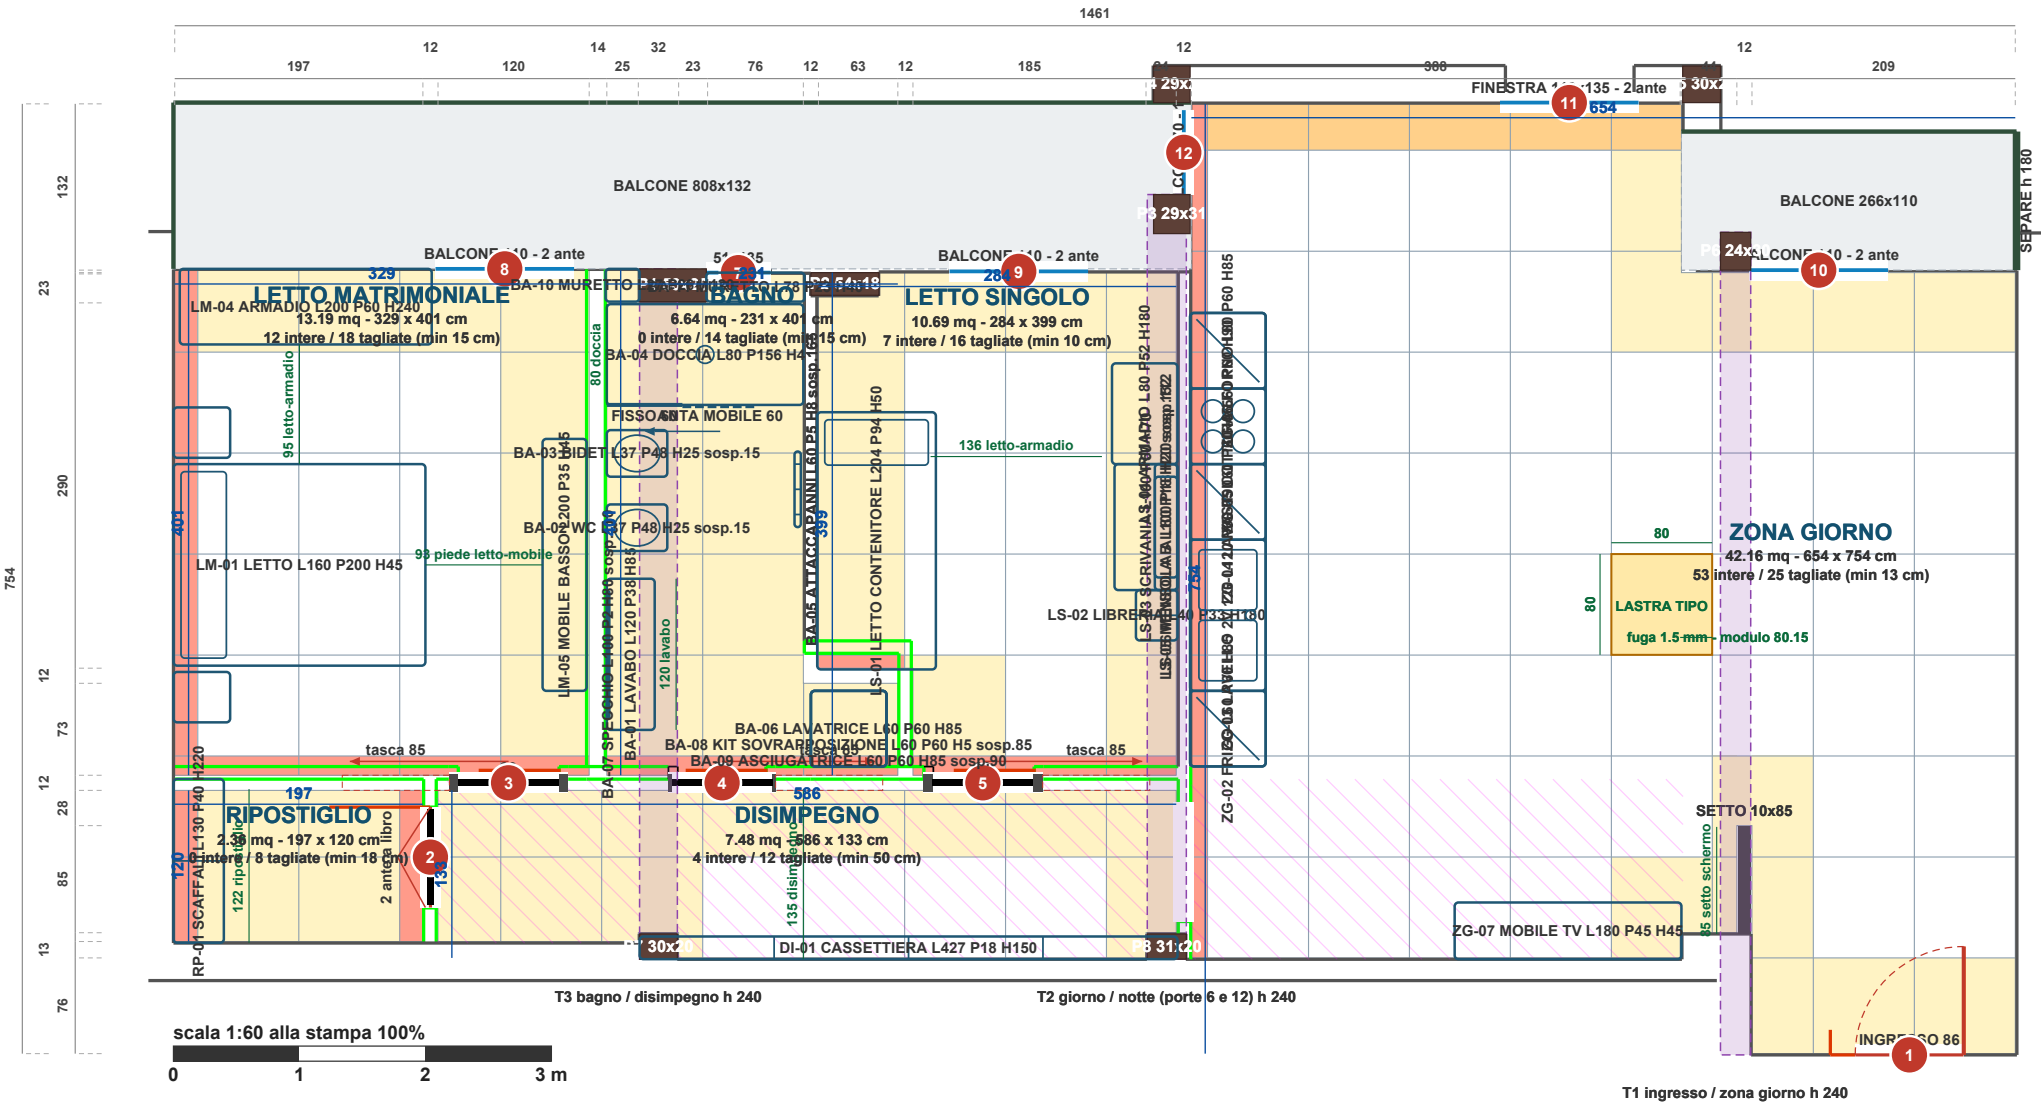

LEGENDA LASTRE

- intera 80x80
- tagliata, lato >= 45 cm (taglio buono)
- tagliata, lato 25-45 cm
- tagliata, lato < 25 cm (listello: da evitare)

CONFRONTO VARIANTI (stessi dati del disegno)									
variante	origine X/Y	lastre intere	tagliate	tagli < 25 cm	tagli 25-45	tagli > 45	lato minimo	% sup. con intere	lastre / sfrido
A	19.3 / 59.0	76	93	30	5	58	10 cm	59%	152 / 15%
B	48.4 / 59.0	77	102	18	32	52	10 cm	60%	162 / 20%
C	19.3 / 22.1	84	100	36	27	37	13 cm	65%	153 / 16%