


APPARTAMENTO - posa gres 80x80 | variante B

B - equilibrata: minimizza i listelli locale per locale (zona giorno pesata x4)  
fuga 1.5 mm - modulo 80.15 cm - griglia unica continua su tutta la casa - battiscopa/rivestimento 1 cm - origine 48.4/59.0 - stampa 100% = 1:60

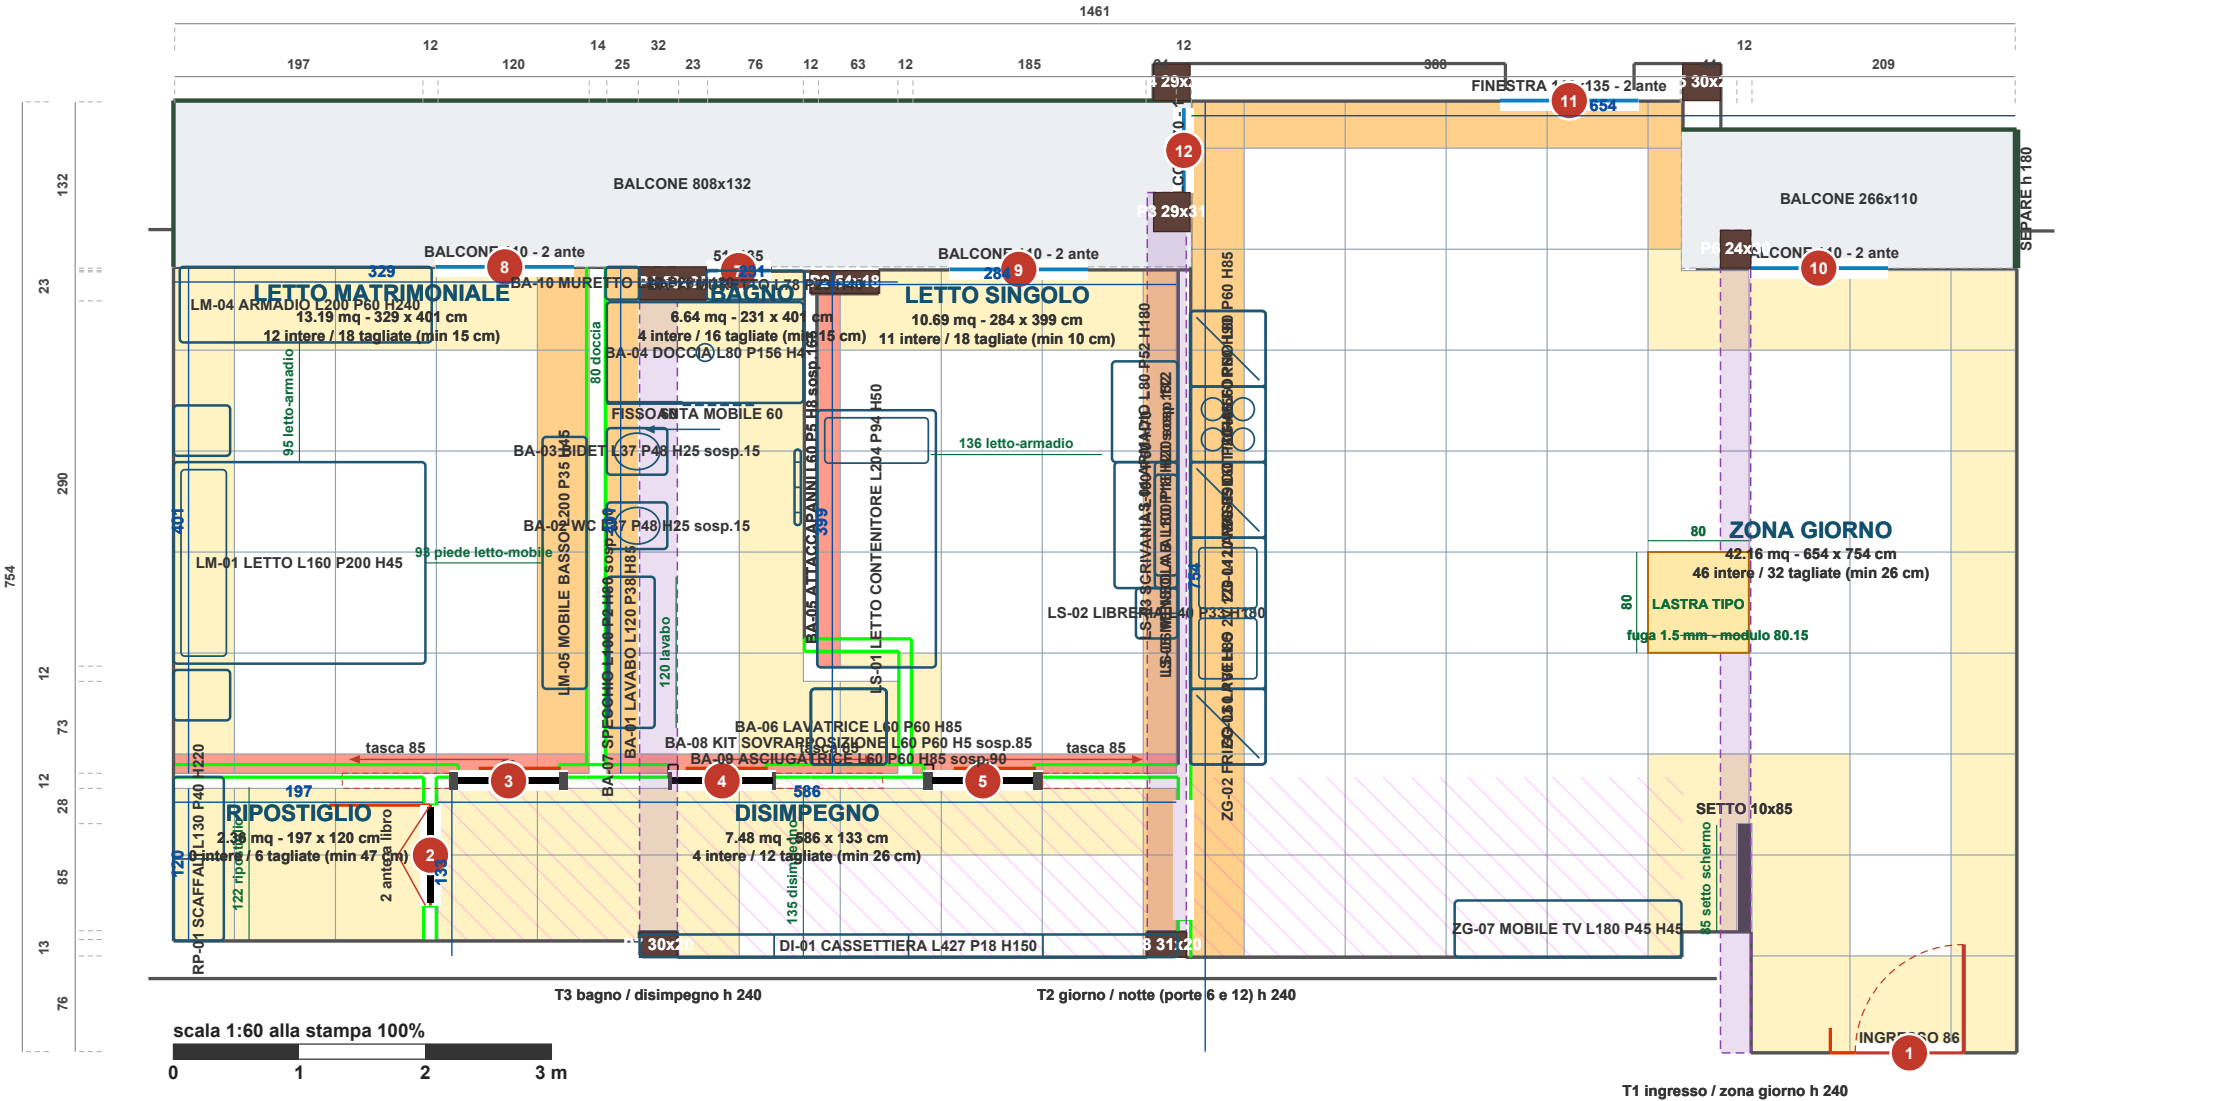

LEGENDA LASTRE

- intera 80x80
- tagliata, lato >= 45 cm (taglio buono)
- tagliata, lato 25-45 cm
- tagliata, lato < 25 cm (listello: da evitare)

CONFRONTO VARIANTI (stessi dati del disegno)

| variante | origine X/Y | lastre intere | tagliate | tagli < 25 cm | tagli 25-45 | tagli > 45 | lato minimo | % sup. con intere | lastre / sfrido |
|----------|-------------|---------------|----------|---------------|-------------|------------|-------------|-------------------|-----------------|
| A        | 19.3 / 59.0 | 76            | 93       | 30            | 5           | 58         | 10 cm       | 59%               | 152 / 15%       |
| B        | 48.4 / 59.0 | 77            | 102      | 18            | 32          | 52         | 10 cm       | 60%               | 162 / 20%       |
| C        | 19.3 / 22.1 | 84            | 100      | 36            | 27          | 37         | 13 cm       | 65%               | 153 / 16%       |