


MURO-SCHERMO ALL'INGRESSO - copertura visiva del fronte cucina

Prolungamento verso l'alto della spalla sinistra del vano d'ingresso (X=1260,3). Visuale calcolata dal punto piu' sfavorevole del vano porta.

Fronte cucina 360 cm - stampa 100% = 1:30

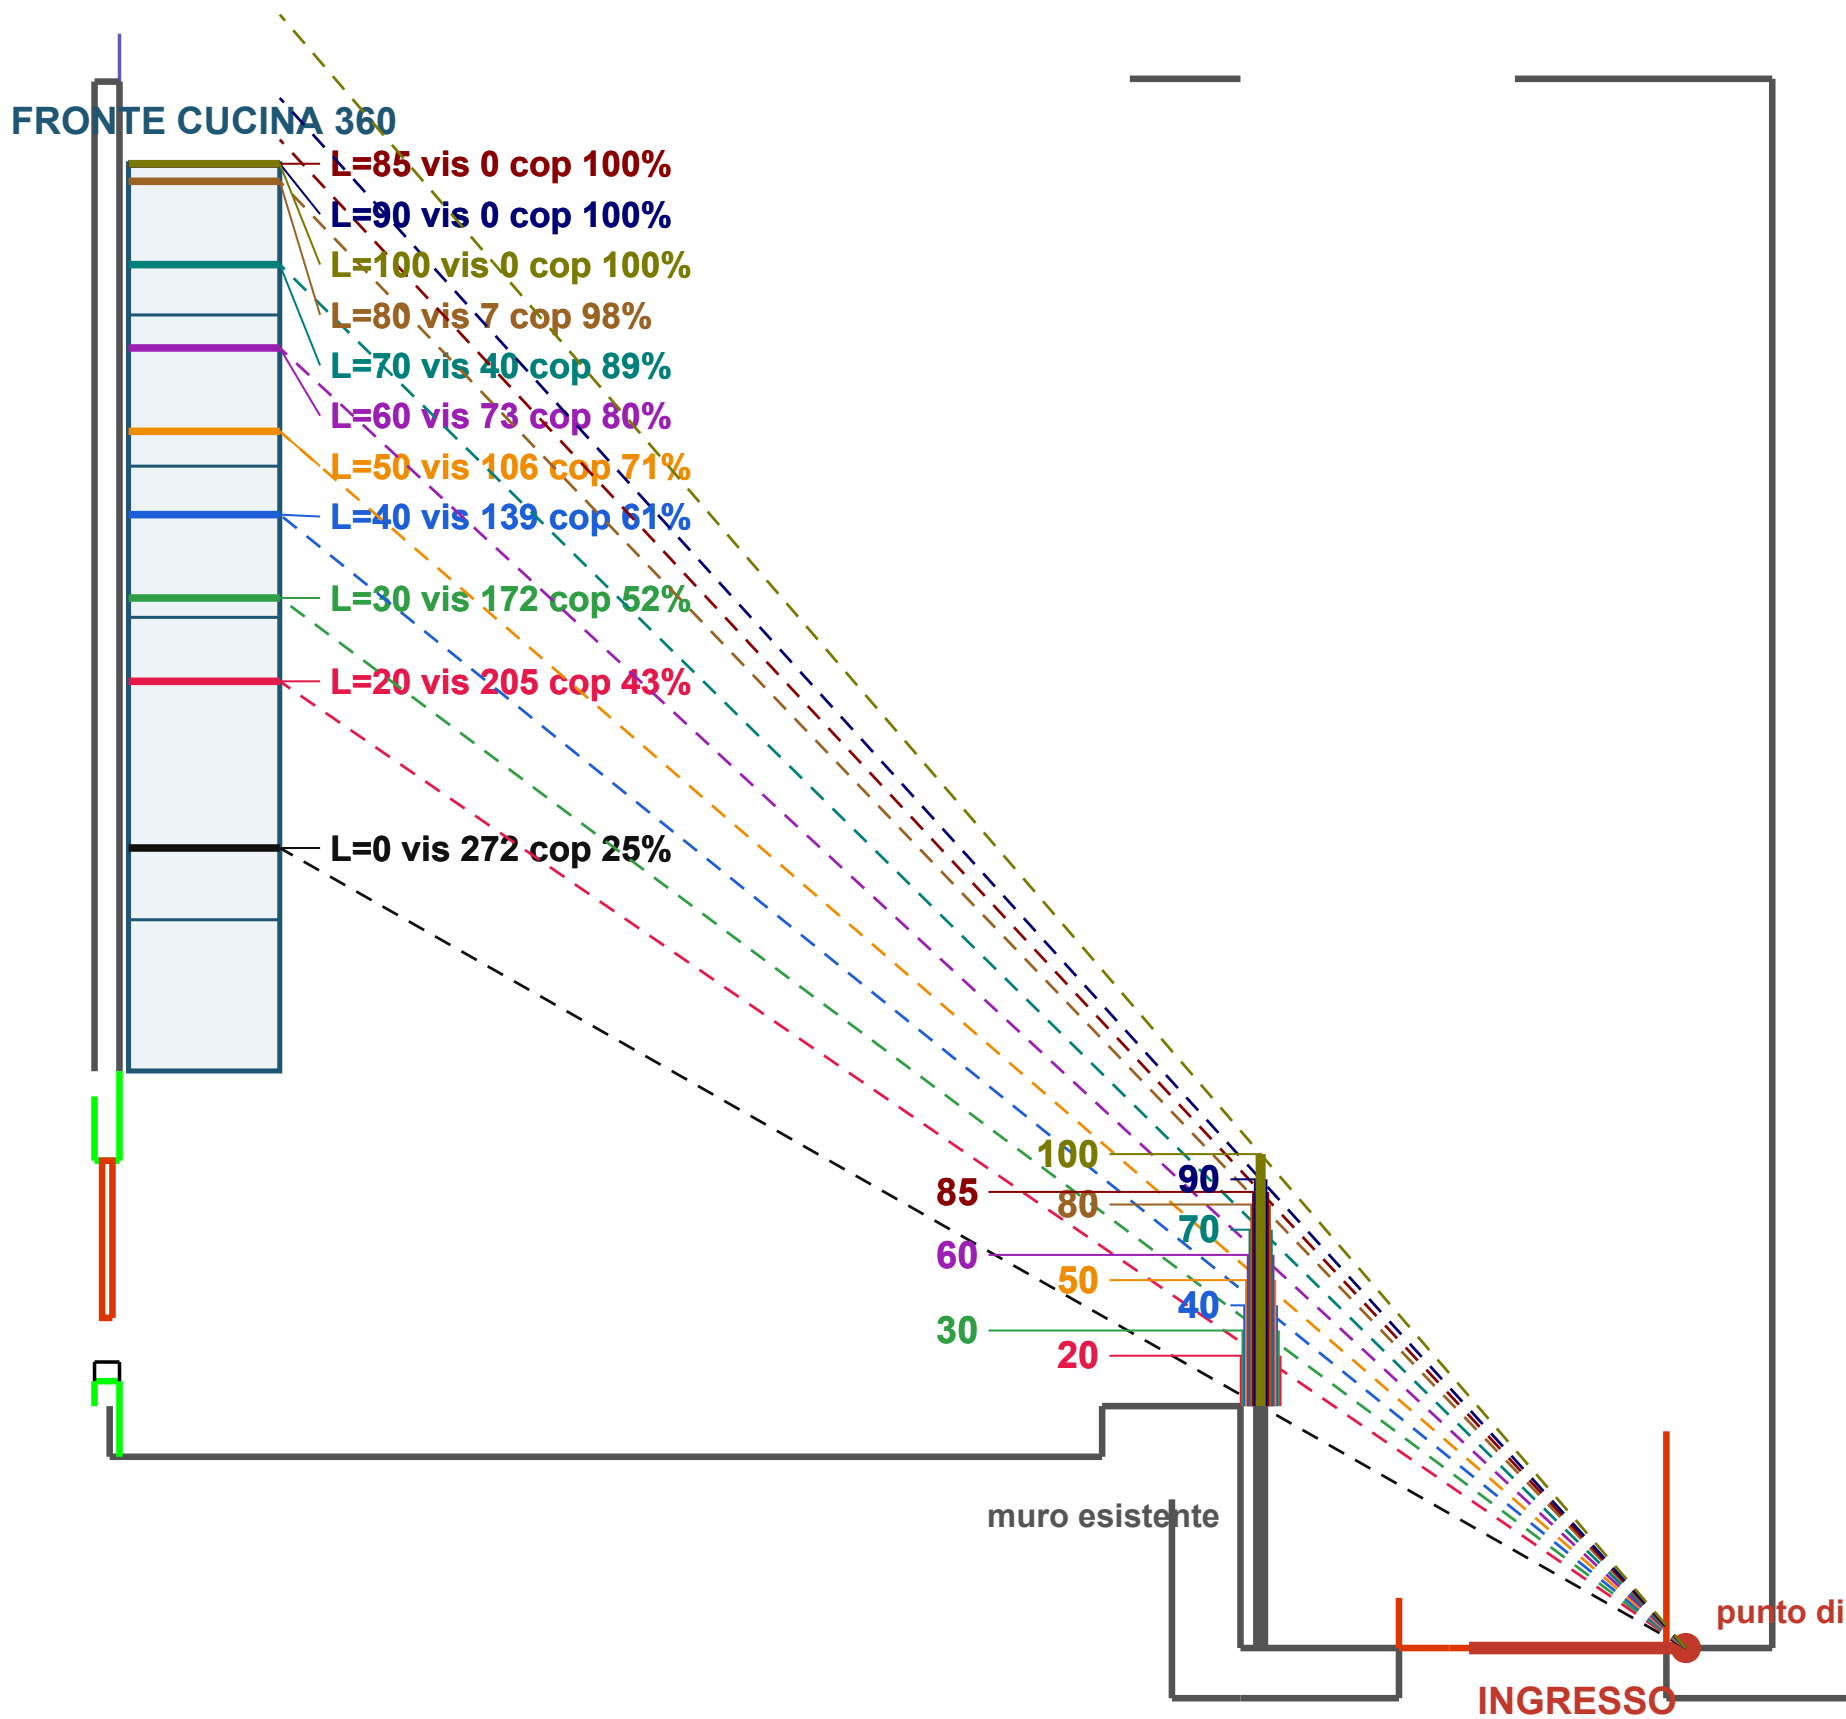

LUNGHEZZE A CONFRONTO

	L = 0 cm	visibile 272 cm	coperto 25%
	L = 20 cm	visibile 205 cm	coperto 43%
	L = 30 cm	visibile 172 cm	coperto 52%
	L = 40 cm	visibile 139 cm	coperto 61%
	L = 50 cm	visibile 106 cm	coperto 71%
	L = 60 cm	visibile 73 cm	coperto 80%
	L = 70 cm	visibile 40 cm	coperto 89%
	L = 80 cm	visibile 7 cm	coperto 98%
	L = 85 cm	visibile 0 cm	coperto 100%
	L = 90 cm	visibile 0 cm	coperto 100%
	L = 100 cm	visibile 0 cm	coperto 100%

SOGLIE

meta' cucina -> muro 28 cm

3/4 di cucina -> muro 55 cm

cucina intera -> muro 82 cm

consigliato 90 cm: copre tutto e cade su una fuga del 90x90 (nessun taglio in piu')