# APPARTAMENTO - posa gres 120x60, 4 corsi a 240, per stanza

**origine di posa ottimale per ogni stanza - minimo numero di lastre e di tagli; rivestimento bagno su 4 corsi a 240**

**fuga 2.0 mm - modulo 120.20 x 60.20 cm - griglia ottimizzata stanza per stanza, soglie divise sotto la porta o alla stanza con piu' margine - battiscopa/rivestimento 1 cm - origine 27.6/33.8 - stampa 100% = 1:60**

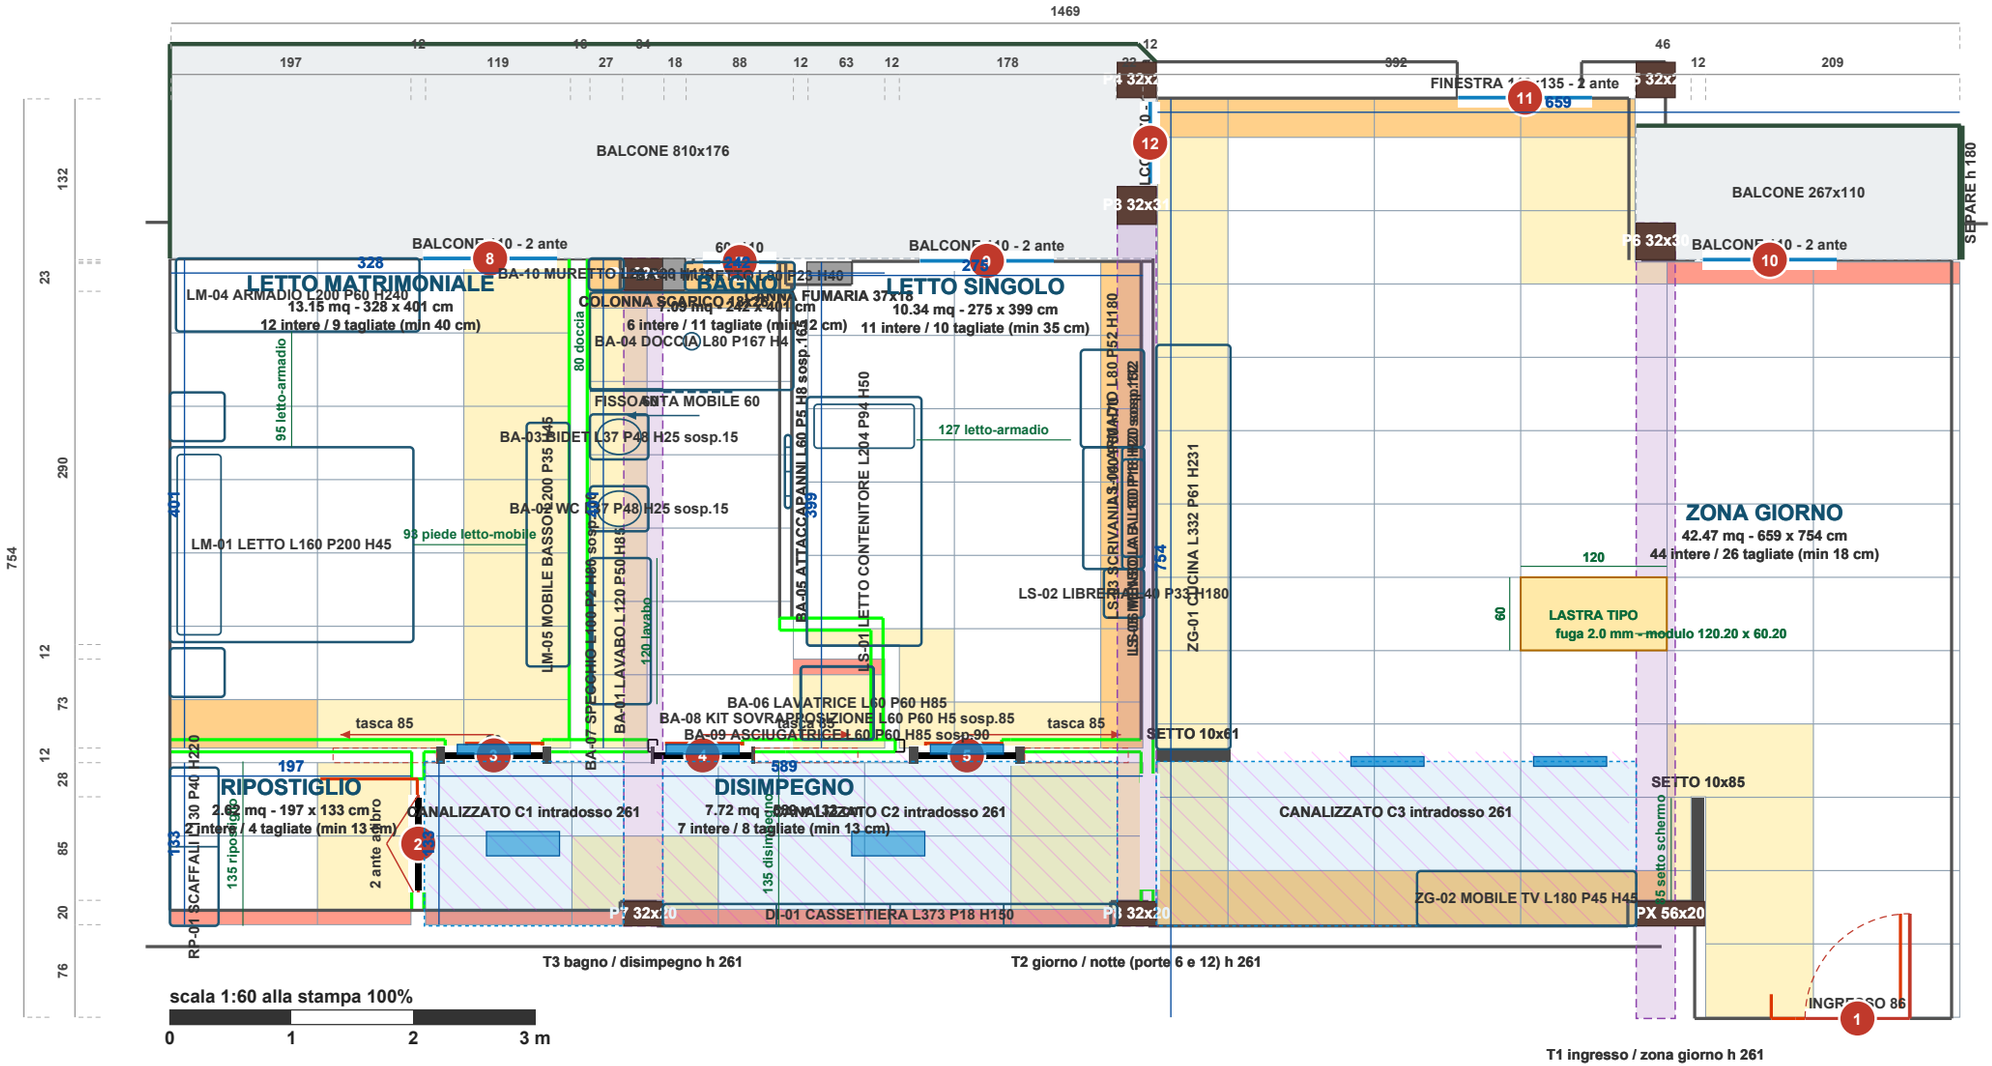


**LEGENDA LASTRE**

- intera 120x60
- tagliata, lato >= 45 cm (taglio buono)
- tagliata, lato 25-45 cm
- tagliata, lato < 25 cm (listello: da evitare)

**CONFRONTO FORMATI (ognuno con la sua origine di posa ottimale)**

| formato | origine X/Y | lastre intere | tagliate | tagli < 25 cm | tagli 25-45 | tagli > 45 | lato minimo | % sup. con intere | lastre / sfrido |
|---|---|---|---|---|---|---|---|---|---|
| 90x90, 3 corsi a filo trave | 26.8 / 24.0 | 63 | 83 | 3 | 45 | 35 | 4 cm | 61% | 123 / 16% |
| 80x80, 4 corsi a filo trave | 37.7 / 74.0 | 70 | 90 | 5 | 25 | 60 | 14 cm | 54% | 148 / 12% |
| 60x60, 4 corsi a 240 | 28.5 / 53.6 | 155 | 121 | 28 | 40 | 53 | 2 cm | 67% | 259 / 11% |
| 60x120, 2 corsi a 240 | 28.5 / 62.2 | 60 | 95 | 4 | 16 | 75 | 2 cm | 52% | 136 / 15% |
| 60x120 pav 120x60 par, 4 corsi a 240 | 28.5 / 62.2 | 60 | 95 | 4 | 16 | 75 | 2 cm | 52% | 136 / 15% |
| 120x60 pav 60x120 par, 2 corsi a 240 | 88.6 / 53.6 | 55 | 94 | 12 | 16 | 66 | 13 cm | 47% | 134 / 14% |
| 120x60, 4 corsi a 240 | 88.6 / 53.6 | 55 | 94 | 12 | 16 | 66 | 13 cm | 47% | 134 / 14% |
| 120x120, 2 corsi a 240, intera all'ingresso | 118.3 / 95.0 | 31 | 76 | 23 | 29 | 24 | 3 cm | 54% | 82 / 29% |
| 60x120, 2 corsi a 240, a filo bagno | 30.5 / 6.2 | 71 | 97 | 32 | 7 | 58 | 1 cm | 61% | 142 / 18% |
| 120x60, 4 corsi a 240, a filo bagno | 31.3 / 5.4 | 63 | 103 | 18 | 12 | 73 | 3 cm | 54% | 139 / 17% |
| 120x60, 4 corsi a 240, per stanza | 27.6 / 33.8 | 82 | 68 | 11 | 18 | 39 | 12 cm | 70% | 134 / 13% |
| 60x120, 2 corsi a 240, per stanza | 28.5 / 62.2 | 84 | 73 | 20 | 24 | 29 | 11 cm | 72% | 137 / 15% |
| 120x60, 4 corsi a 240, sfalsata 1/2 | 29.1 / 53.6 | 57 | 101 | 14 | 23 | 64 | 2 cm | 49% | 134 / 14% |
| 120x60, 4 corsi a 240, sfalsata 1/3 | 117.9 / 53.6 | 60 | 101 | 18 | 29 | 54 | 11 cm | 52% | 141 / 18% |
| 60x120, 2 corsi a 240, sfalsata 1/2 | 28.5 / 56.7 | 59 | 99 | 14 | 19 | 66 | 2 cm | 51% | 136 / 15% |
| 60x120, 2 corsi a 240, sfalsata 1/3 | 28.5 / 102.3 | 62 | 100 | 13 | 28 | 59 | 2 cm | 54% | 142 / 18% |