


APPARTAMENTO - posa gres 120x60

origine di posa ottimale 88.6 / 53.6 cm - minimo numero di lastre e di tagli; rivestimento bagno su 5 corsi a filo trave
fuga 2.0 mm - modulo 120.20 x 60.20 cm - griglia unica continua su tutta la casa - battiscopa/rivestimento 1 cm - origine 88.6/53.6 - stampa 100% = 1:60

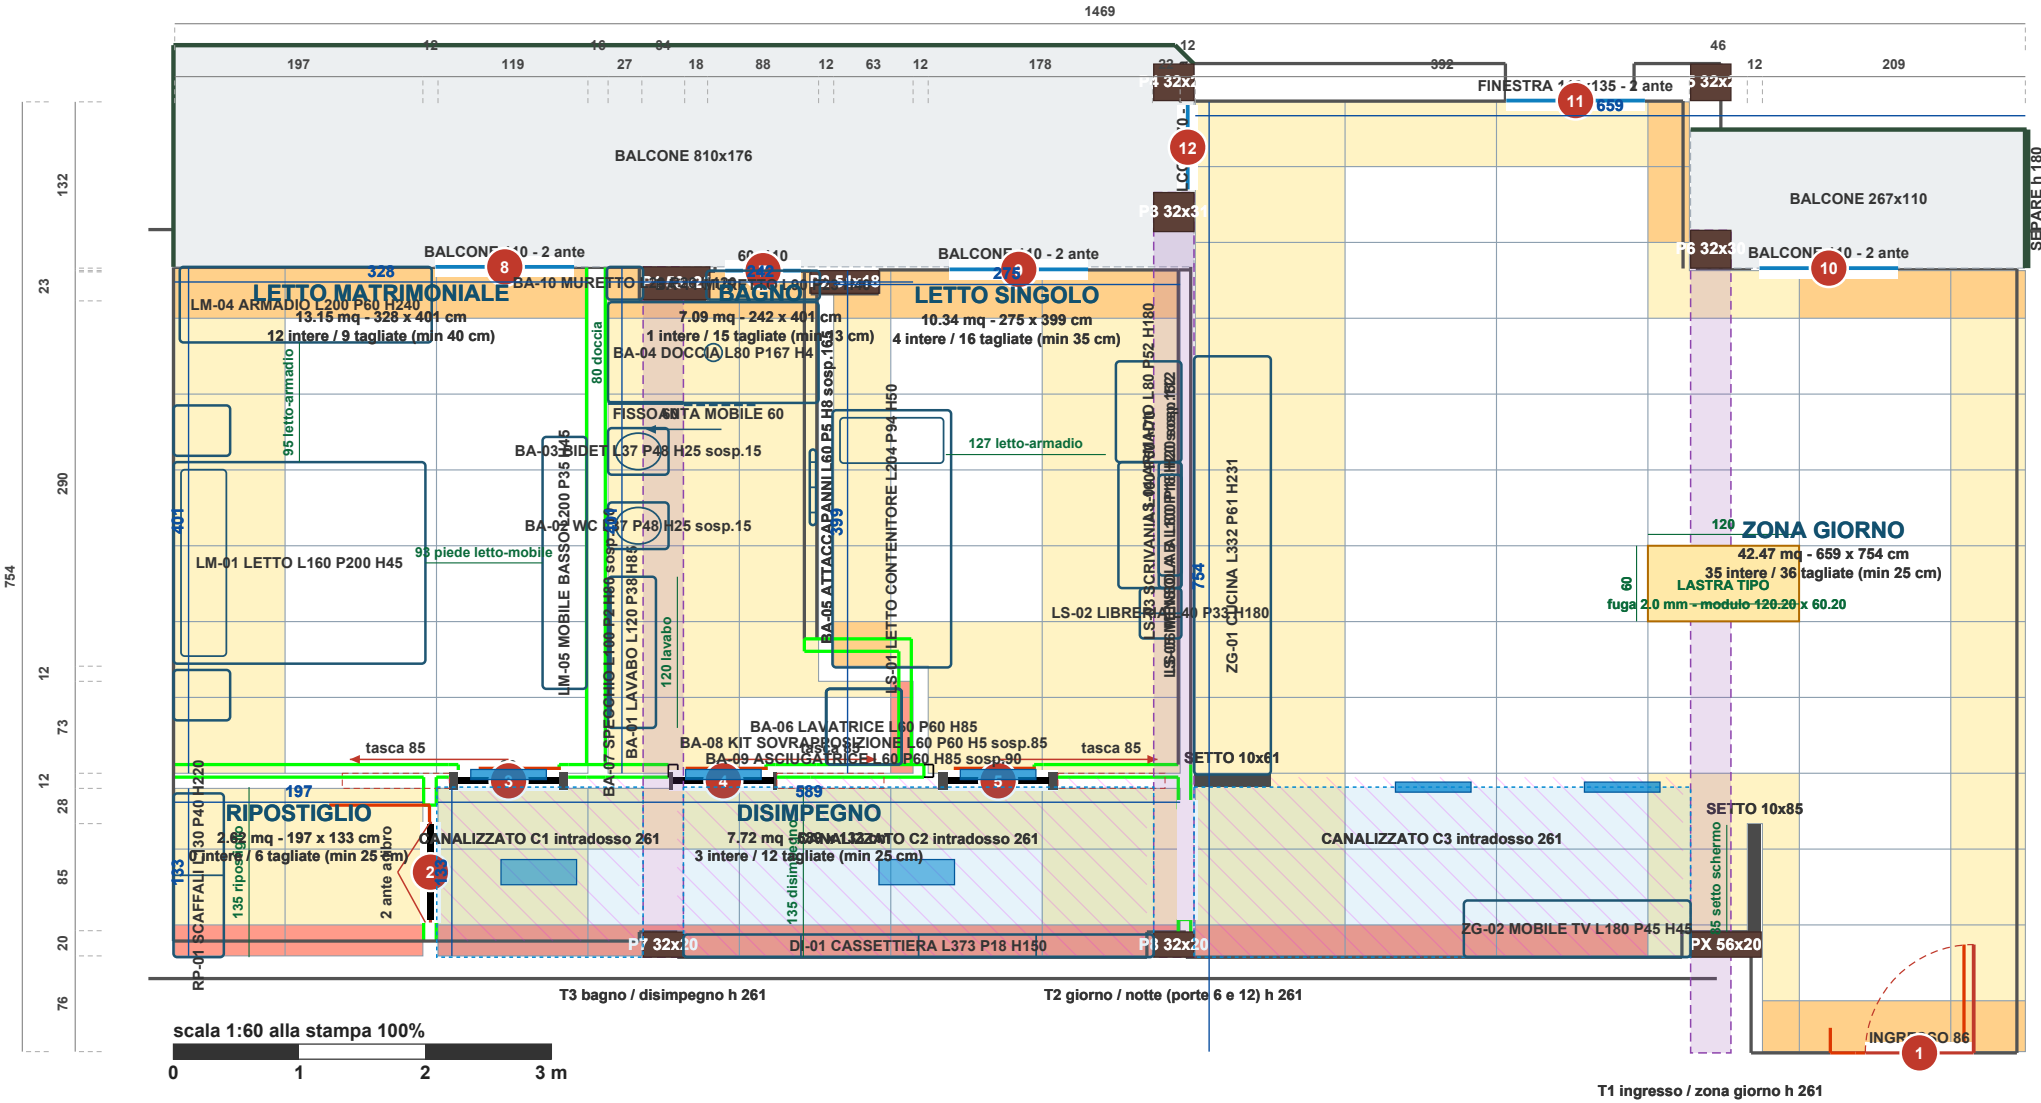

LEGENDA LASTRE

- intera 120x60
- tagliata, lato >= 45 cm (taglio buono)
- tagliata, lato 25-45 cm
- tagliata, lato < 25 cm (listello: da evitare)

CONFRONTO FORMATI (ognuno con la sua origine di posa ottimale)										
formato	origine X/Y	lastre intere	tagliate	tagli < 25 cm	tagli 25-45	tagli > 45	lato minimo	% sup. con intere	lastre / sfrido	
90x90, 3 corsi a filo trave	26.8 / 24.0	63	83	3	45	35	4 cm	61%	123 / 16%	
80x80, 4 corsi a filo trave	37.7 / 74.0	70	90	5	25	60	14 cm	54%	148 / 12%	
60x60, 5 corsi a filo trave	28.5 / 53.6	155	121	28	40	53	2 cm	67%	259 / 11%	
60x120, 3 corsi a filo trave	28.5 / 62.2	60	95	4	16	75	2 cm	52%	136 / 15%	
60x120, 3 corsi a filo trave	28.5 / 62.2	60	95	4	16	75	2 cm	52%	136 / 15%	