


APPARTAMENTO - posa gres 80x80 | variante B

B - zona giorno prioritaria: massimo numero di lastre intere nell'ambiente principale
fuga 1.5 mm - modulo 80.15 cm - griglia unica continua su tutta la casa - battiscopa/rivestimento 1 cm - origine 19.3/22.1 - stampa 100% = 1:60

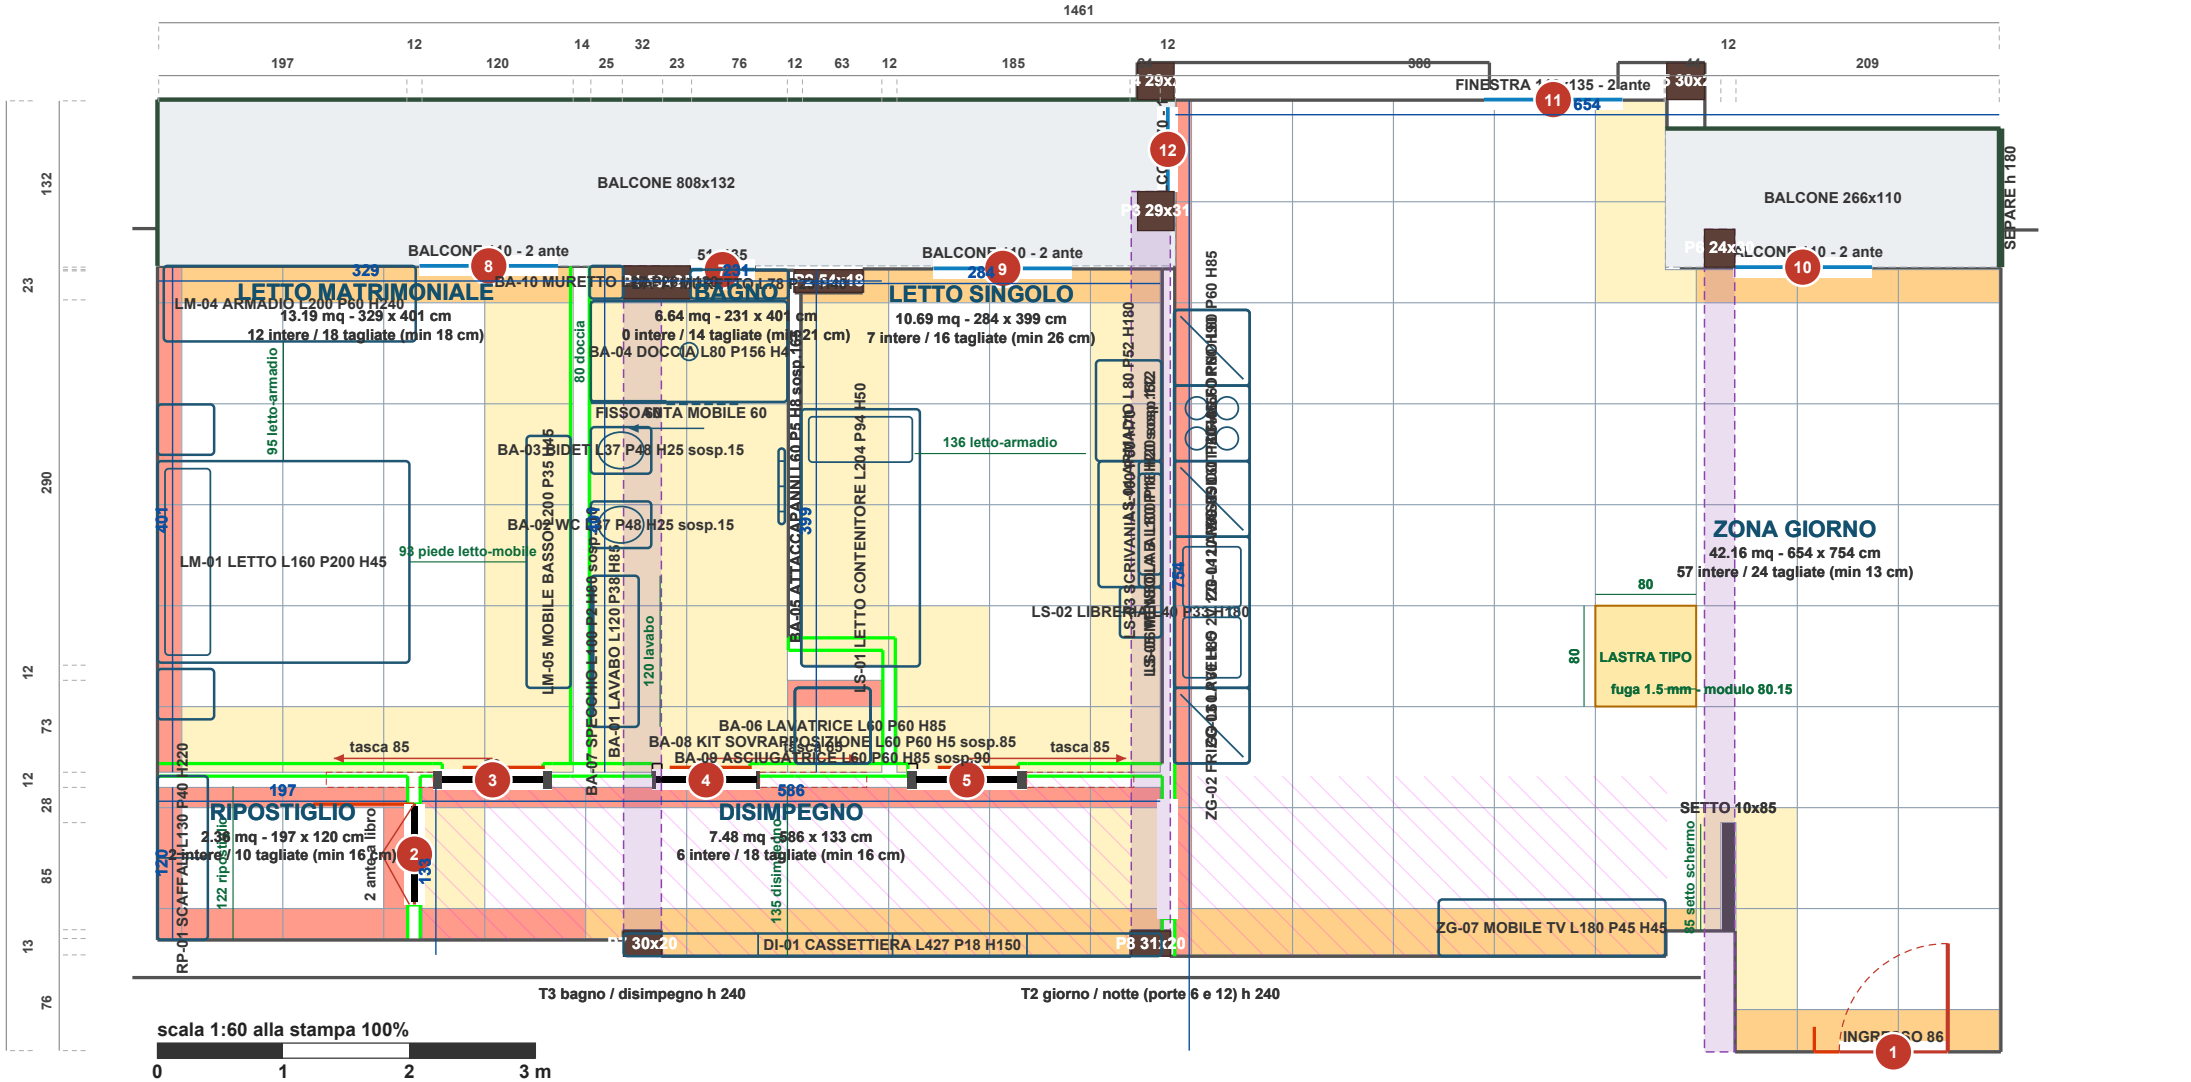

LEGENDA LASTRE

- intera 80x80
- tagliata, lato >= 45 cm (taglio buono)
- tagliata, lato 25-45 cm
- tagliata, lato < 25 cm (listello: da evitare)

CONFRONTO VARIANTI (stessi dati del disegno)									
variante	origine X/Y	lastre intere	tagliate	tagli < 25 cm	tagli 25-45	tagli > 45	lato minimo	% sup. con intere	lastre / sfrido
A	48.4 / 59.0	77	102	18	32	52	10 cm	60%	162 / 20%
B	19.3 / 22.1	84	100	36	27	37	13 cm	65%	153 / 16%
C	6.5 / 22.2	92	104	46	29	29	3 cm	71%	159 / 19%