


APPARTAMENTO - posa gres 60x120

origine di posa ottimale 28.5 / 62.2 cm - minimo numero di lastre e di tagli; rivestimento bagno su 4 corsi a 240
fuga 2.0 mm - modulo 60.20 x 120.20 cm - griglia unica continua su tutta la casa - battiscopa/rivestimento 1 cm - origine 28.5/62.2 - stampa 100% = 1:60

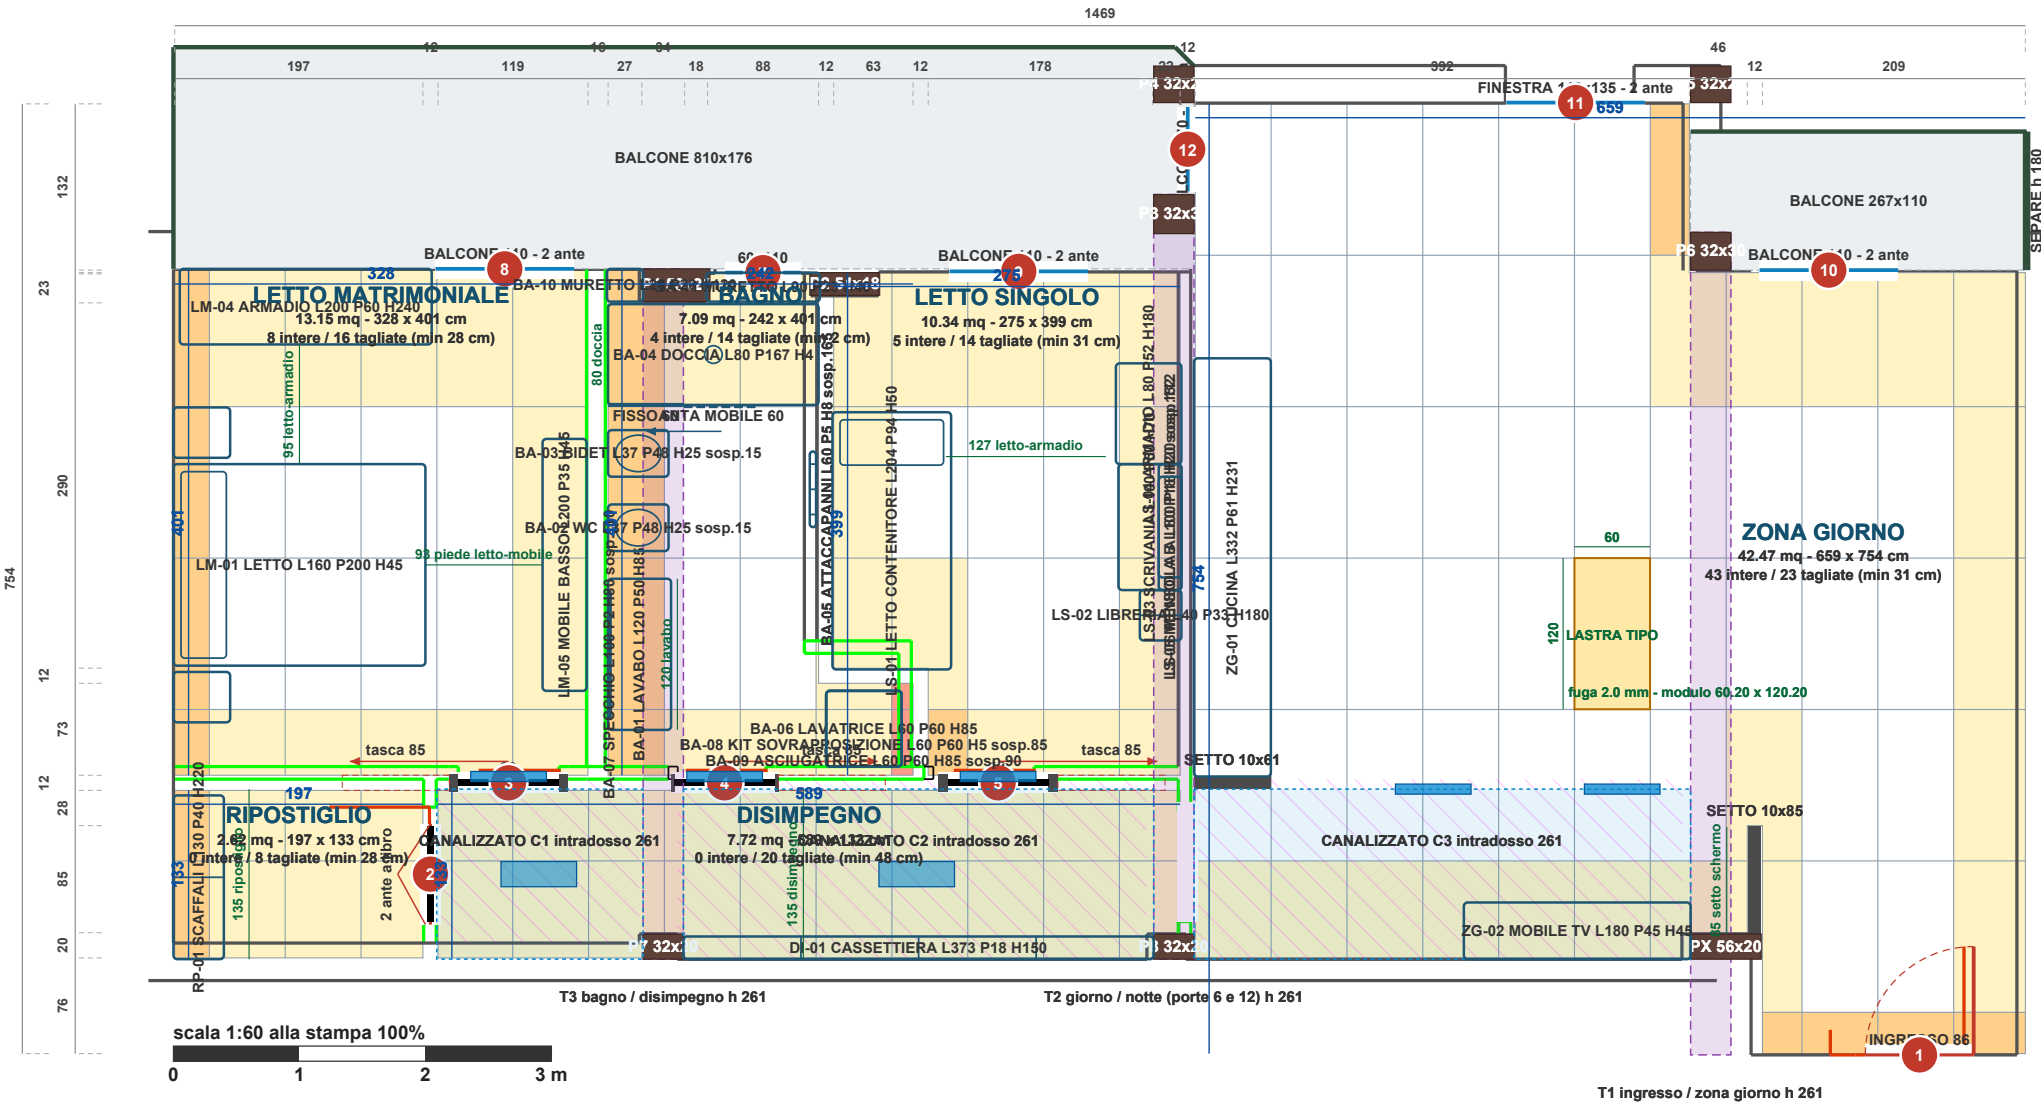

LEGENDA LASTRE

- intera 60x120
- tagliata, lato >= 45 cm (taglio buono)
- tagliata, lato 25-45 cm
- tagliata, lato < 25 cm (listello: da evitare)

CONFRONTO FORMATI (ognuno con la sua origine di posa ottimale)										
formato	origine X/Y	lastre intere	tagliate	tagli < 25 cm	tagli 25-45	tagli > 45	lato minimo	% sup. con intere	lastre / sfrido	
90x90, 3 corsi a filo trave	26.8 / 24.0	63	83	3	45	35	4 cm	61%	123	16%
80x80, 4 corsi a filo trave	37.7 / 74.0	70	90	5	25	60	14 cm	54%	148	12%
60x60, 4 corsi a 240	28.5 / 53.6	155	121	28	40	53	2 cm	67%	259	11%
60x120, 2 corsi a 240	28.5 / 62.2	60	95	4	16	75	2 cm	52%	136	15%
60x120 pav.120x60 par. 4 corsi a 240	28.5 / 62.2	60	95	4	16	75	2 cm	52%	136	15%